


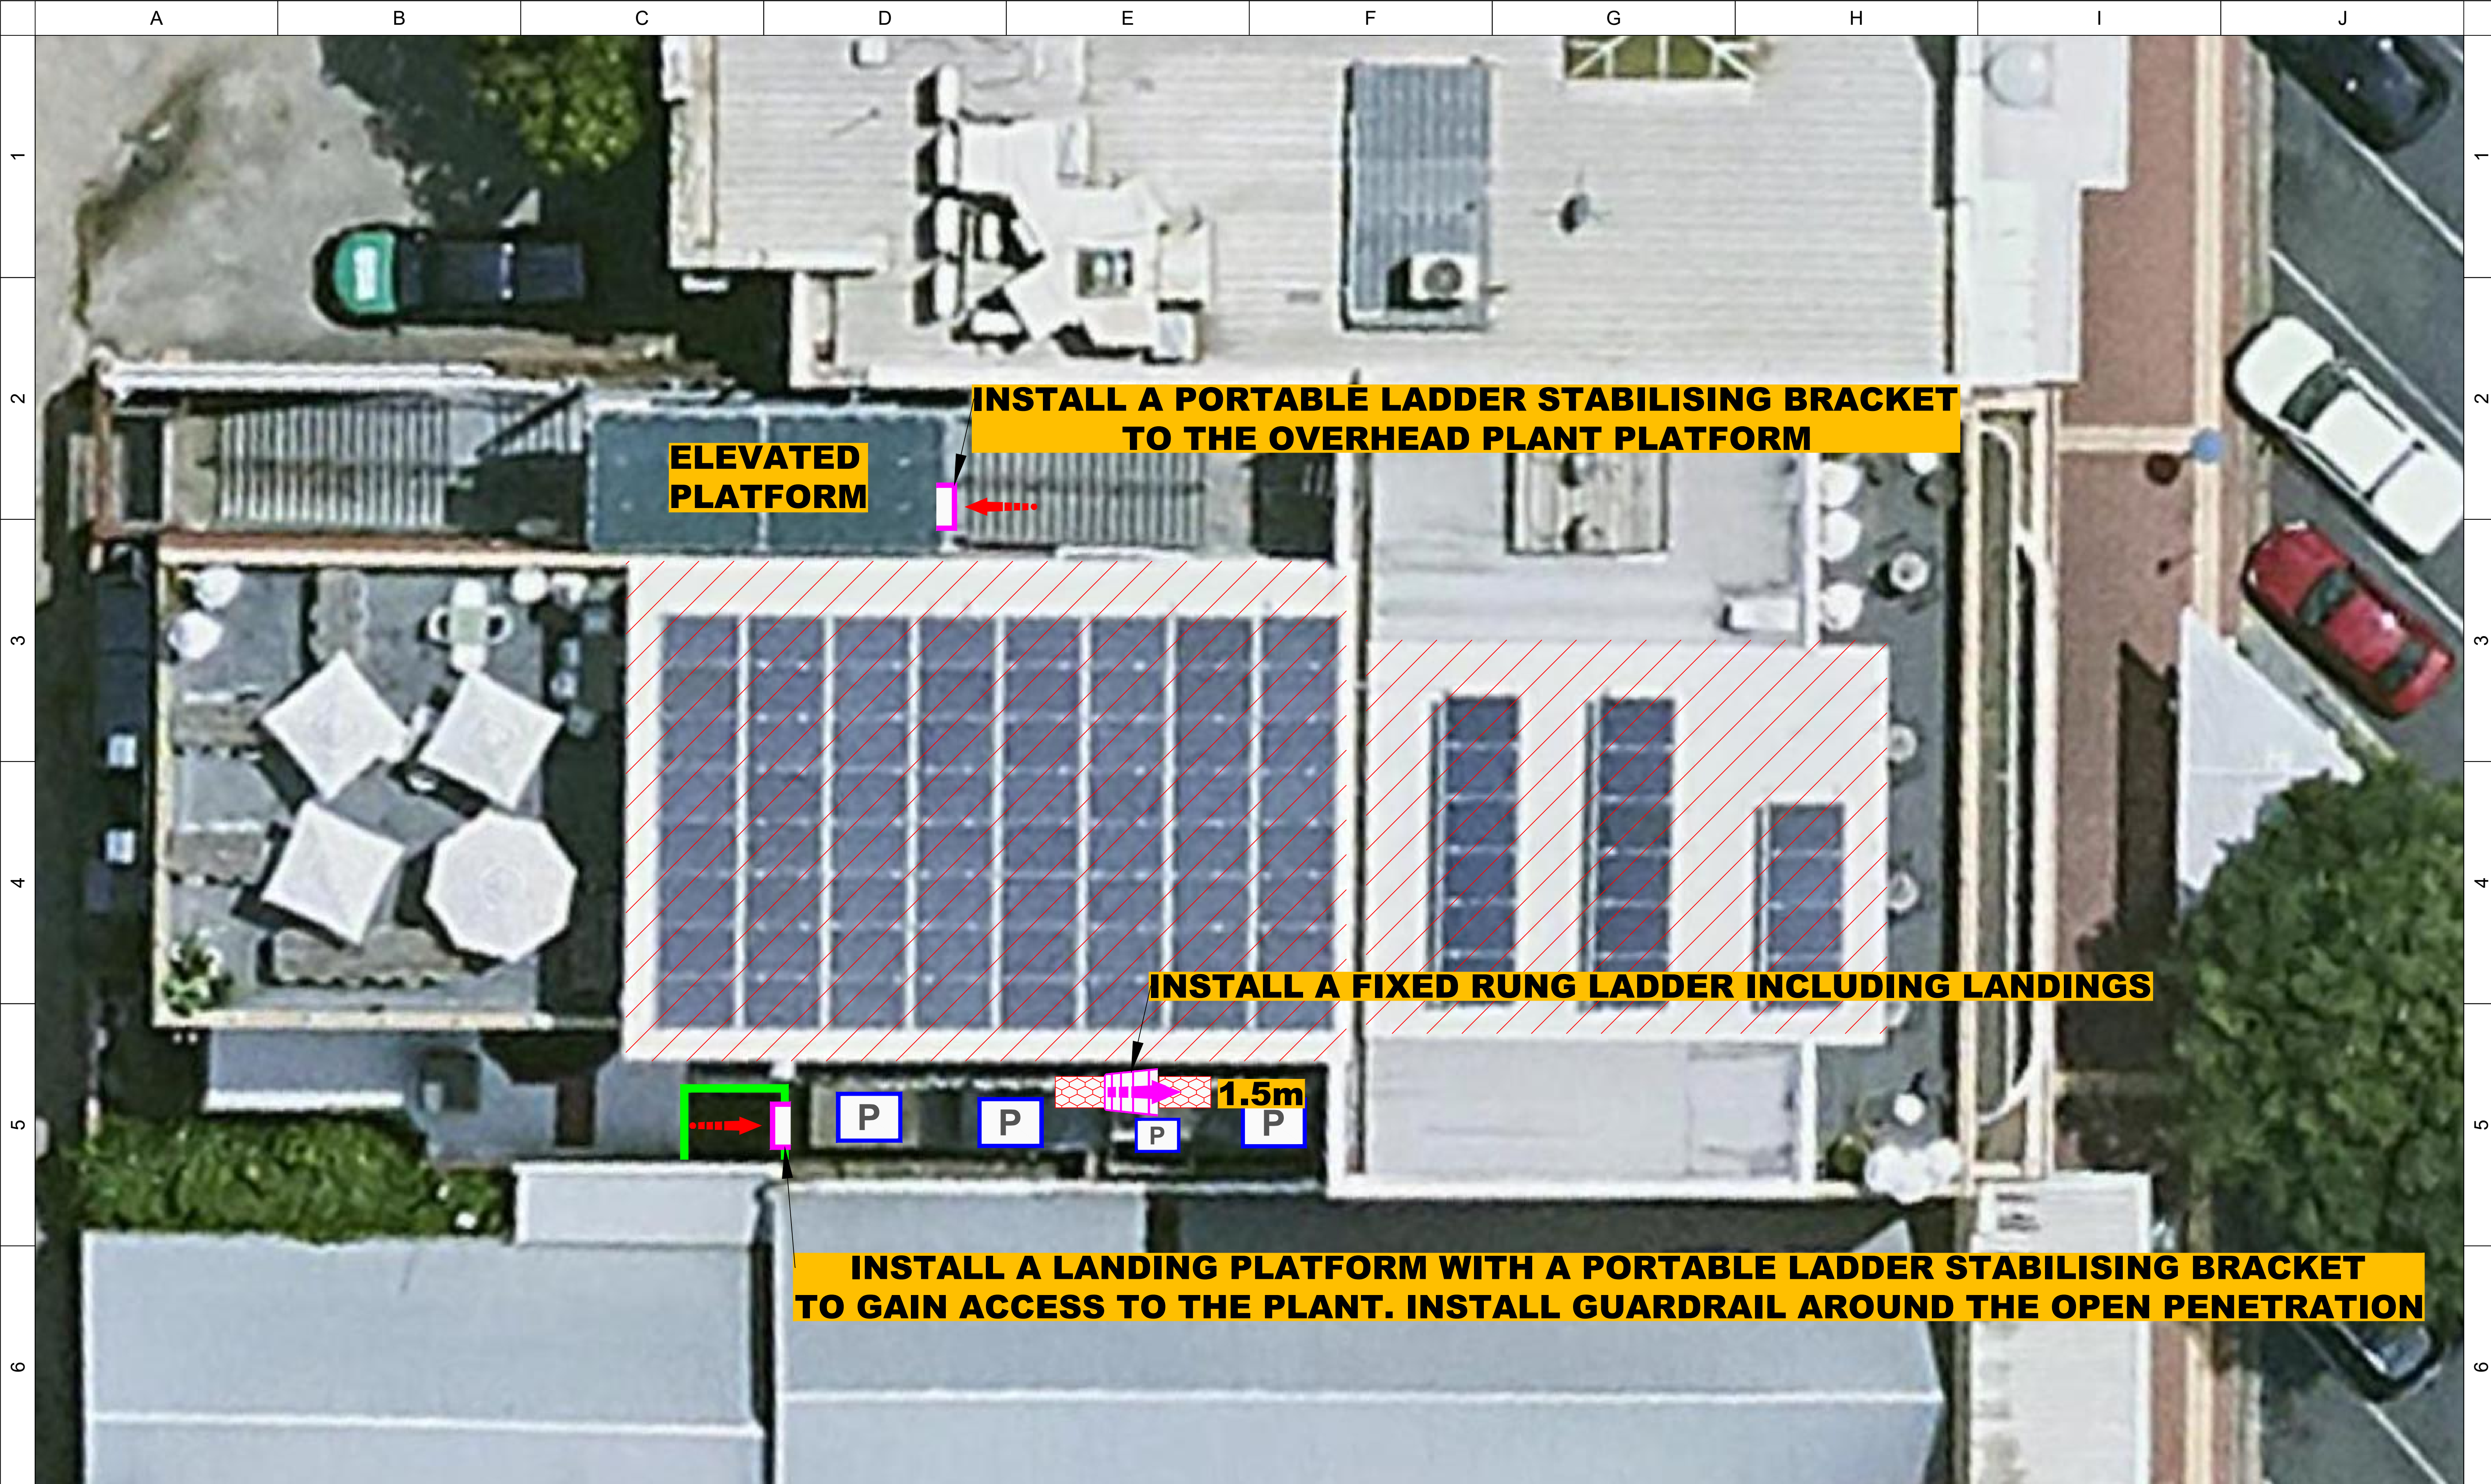

7	Date	07-03-2025				Existing line marking and signage is indicative only	DECOMMISSIONED ITEM DEMARCATION LINE ANCHOR STOP ROOF ACCESS SIGNAGE TRAFFICABLE LASERLITE COVER	ROOF ACCESS POINT ACCESS HATCH WITH GUARDRAIL STAINLESS STEEL ANCHOR POINT DAVIT SOCKET ROOF NEEDLE STL - STAINLESS STEEL STATIC LINE RR - ALUMINIUM MONORAIL SYSTEM ALUMINIUM GUARDRAIL SELF CLOSING GATE ACCESS FROM THE GROUND HIGH RISK AREA - NO ACCESS SAFETY SIGNAGE	LB - LADDER STABILIZING BRACKET CSL - STEP TYPE LADDER WITH CAGE SL - STEP TYPE LADDER CRL - RUNG LADDER WITH CAGE RL - RUNG TYPE LADDER STEP BRIDGE OVER PARAPET WALKWAY FLAT SP - WALKWAY PLATFORM ST - STAIRWAY SS - SINGLE STEP SKYLIGHT PROTECTION BLUE COLOUR DENOTES EXISTING SYSTEMS				
	DESC.	Initial Release					Company: Australian Venue Co.	Stage: Risk Assessment Date: 07/03/2025					
	Rev	00					Site: ALB - Albion Hotel 593 Dean St, Albury NSW 2640	Drawn: AS Check: GC					
							Work area: Main Building Site No:	Scale: NTS					
	A				B	C	D	E	F	G	H	I	J
Verify all dimensions and site measure before commencing work. Do not scale from this drawing. This drawing is copyright and remains the property of Workplace Access and Safety and shall not be reproduced or copied in any format by any means without the written permissions of Workplace Access and Safety. Template V 07.5/2020													