


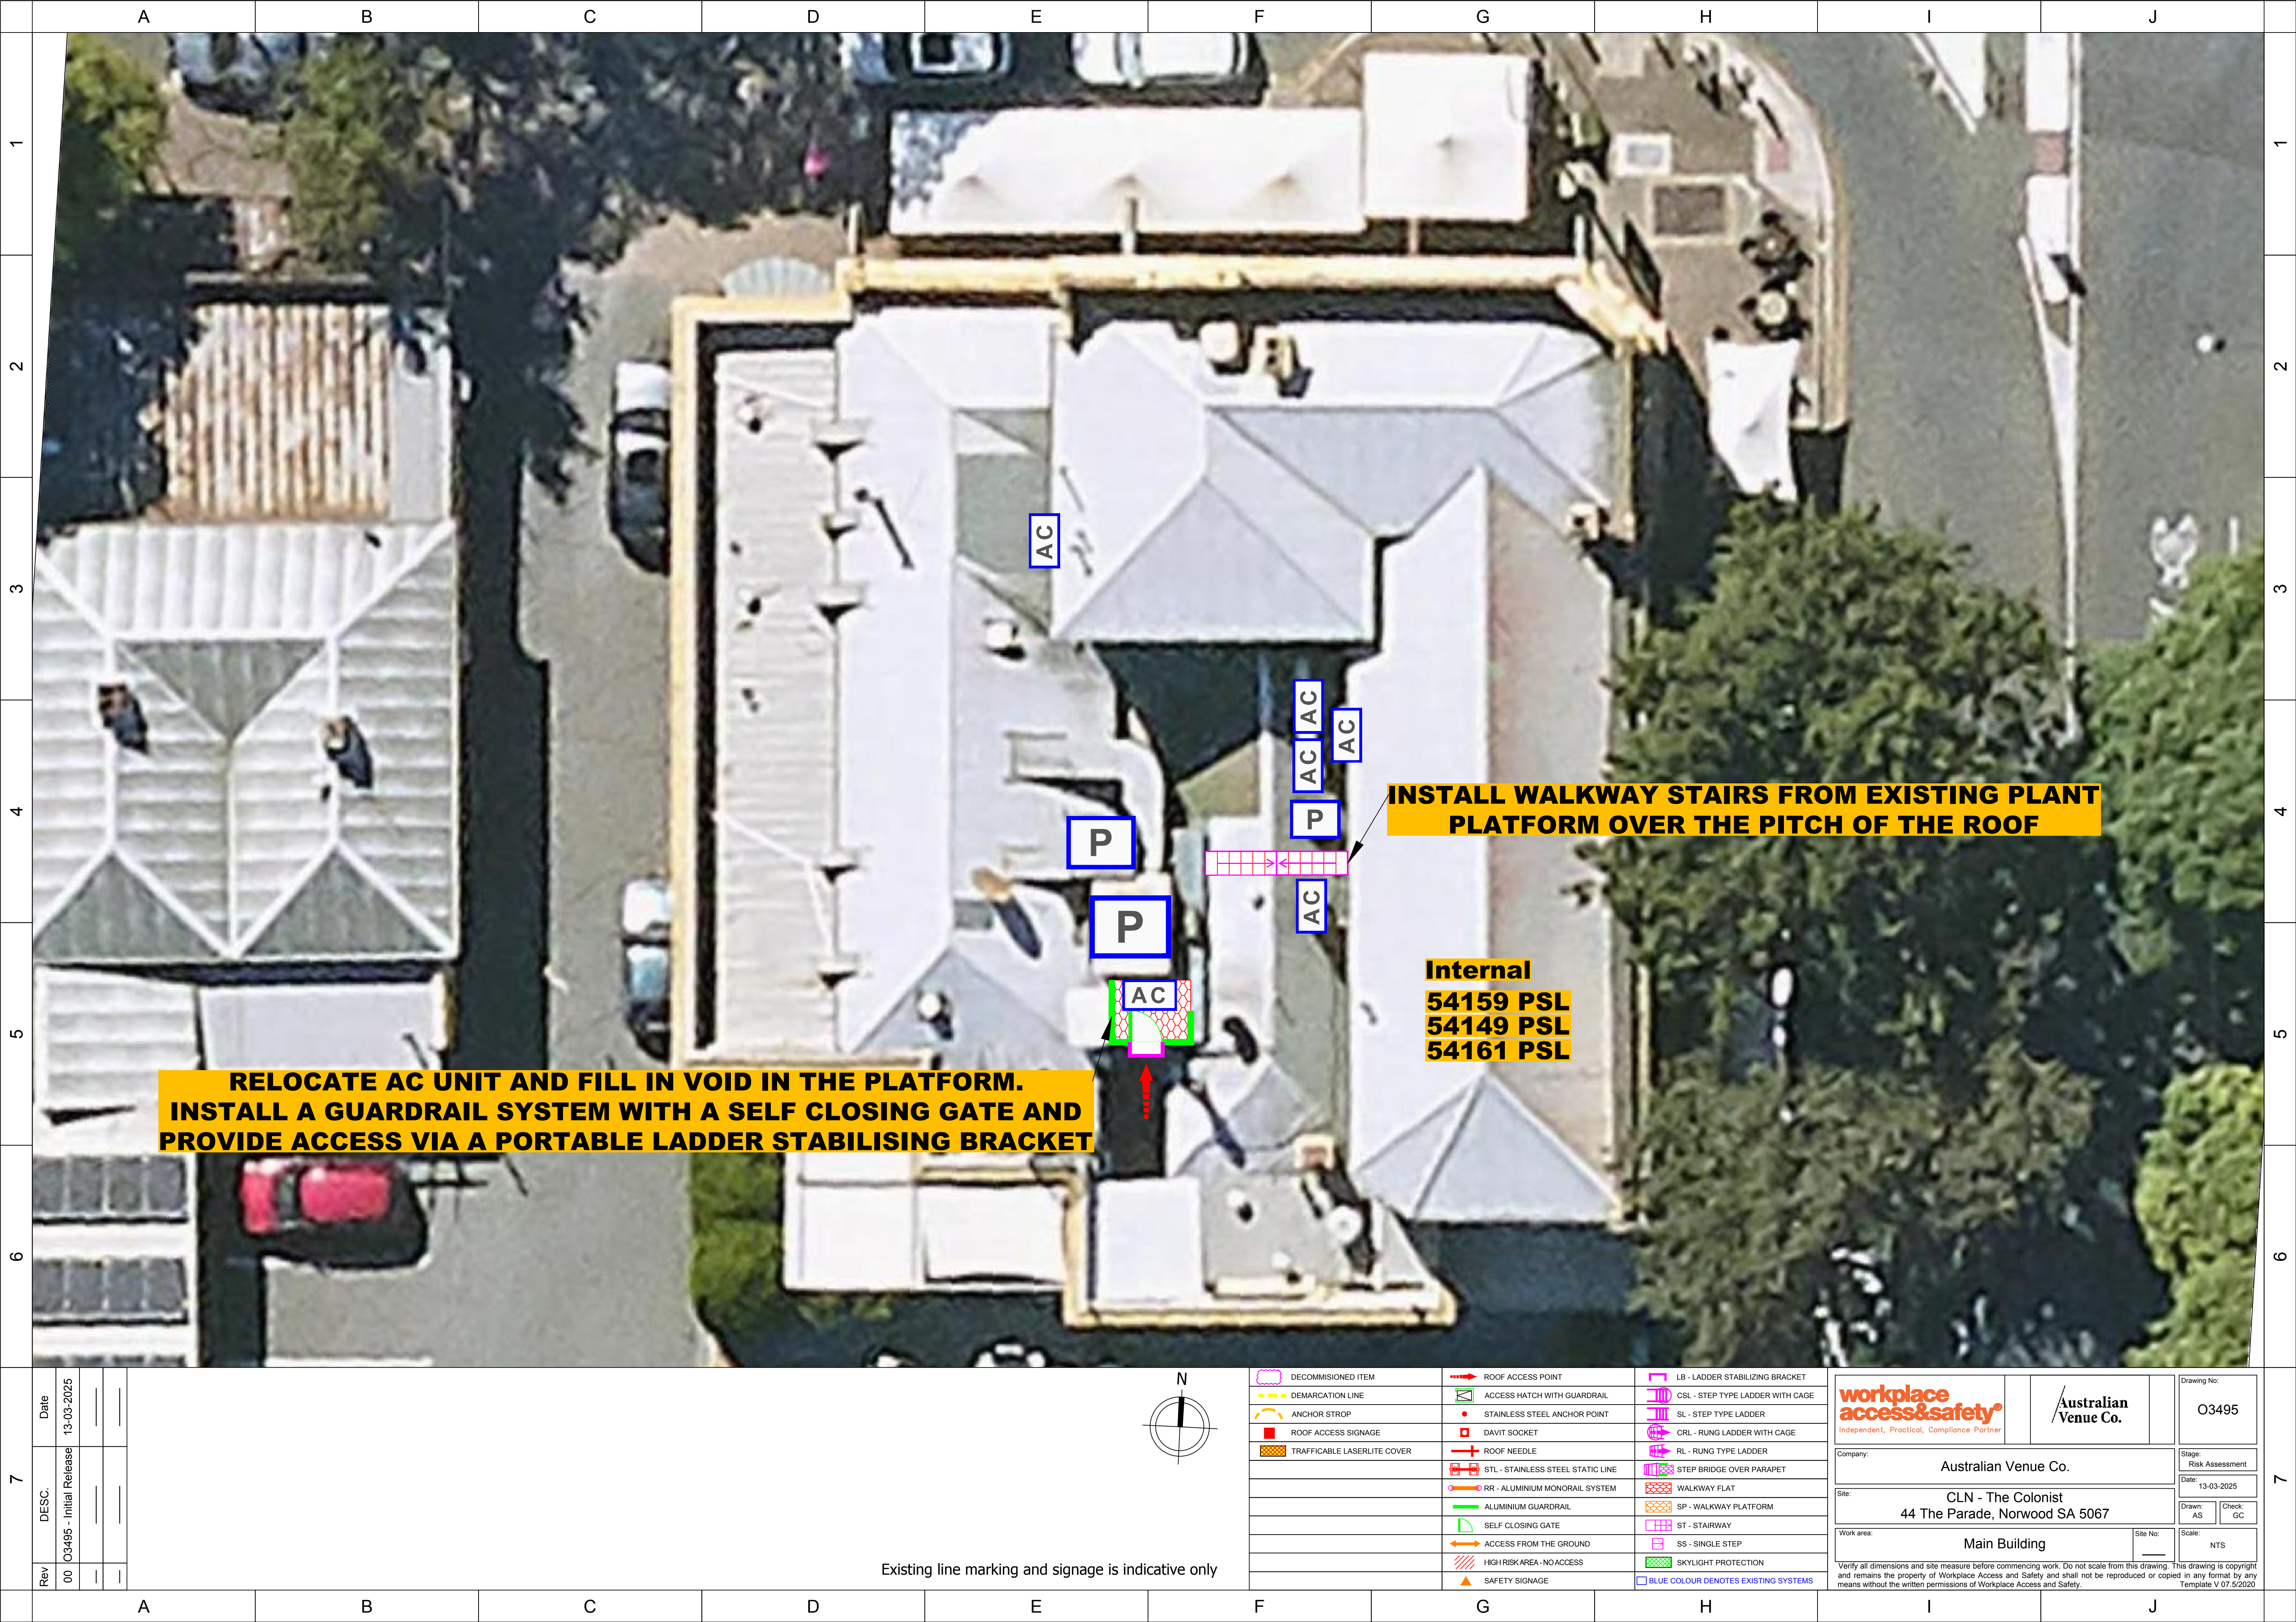

RELOCATE AC UNIT AND FILL IN VOID IN THE PLATFORM.
INSTALL A GUARDRAIL SYSTEM WITH A SELF CLOSING GATE AND
PROVIDE ACCESS VIA A PORTABLE LADDER STABILISING BRACKET

INSTALL WALKWAY STAIRS FROM EXISTING PLANT
PLATFORM OVER THE PITCH OF THE ROOF

Internal
54159 PSL
54149 PSL
54161 PSL

	DECOMMISSIONED ITEM		ROOF ACCESS POINT		LB - LADDER STABILIZING BRACKET
	DEMARICATION LINE		ACCESS HATCH WITH GUARDRAIL		CSL - STEP TYPE LADDER WITH CAGE
	ANCHOR STROP		STAINLESS STEEL ANCHOR POINT		SL - STEP TYPE LADDER
	ROOF ACCESS SIGNAGE		DAVIT SOCKET		CRL - RUNG LADDER WITH CAGE
	TRAFFICABLE LASERLITE COVER		ROOF NEEDLE		RL - RUNG TYPE LADDER
			STL - STAINLESS STEEL STATIC LINE		SB - STEP BRIDGE OVER PARAPET
			RR - ALUMINIUM MONORAIL SYSTEM		WALKWAY FLAT
			ALUMINIUM GUARDRAIL		SP - WALKWAY PLATFORM
			SELF CLOSING GATE		ST - STAIRWAY
			ACCESS FROM THE GROUND		SS - SINGLE STEP
			HIGH RISK AREA - NO ACCESS		SKYLIGHT PROTECTION
			SAFETY SIGNAGE		BLUE COLOUR DENOTES EXISTING SYSTEMS

				Drawing No: O3495	
Company: Australian Venue Co.				Stage: Risk Assessment	
Site: CLN - The Colonist 44 The Parade, Norwood SA 5067				Date: 13-03-2025	
Work area: Main Building				Drawn: AS	
				Check: GC	
				Scale: NTS	
Verify all dimensions and site measure before commencing work. Do not scale from this drawing. This drawing is copyright and remains the property of Workplace Access and Safety and shall not be reproduced or copied in any format by any means without the written permissions of Workplace Access and Safety. Template V 07.5/2020					

Existing line marking and signage is indicative only