


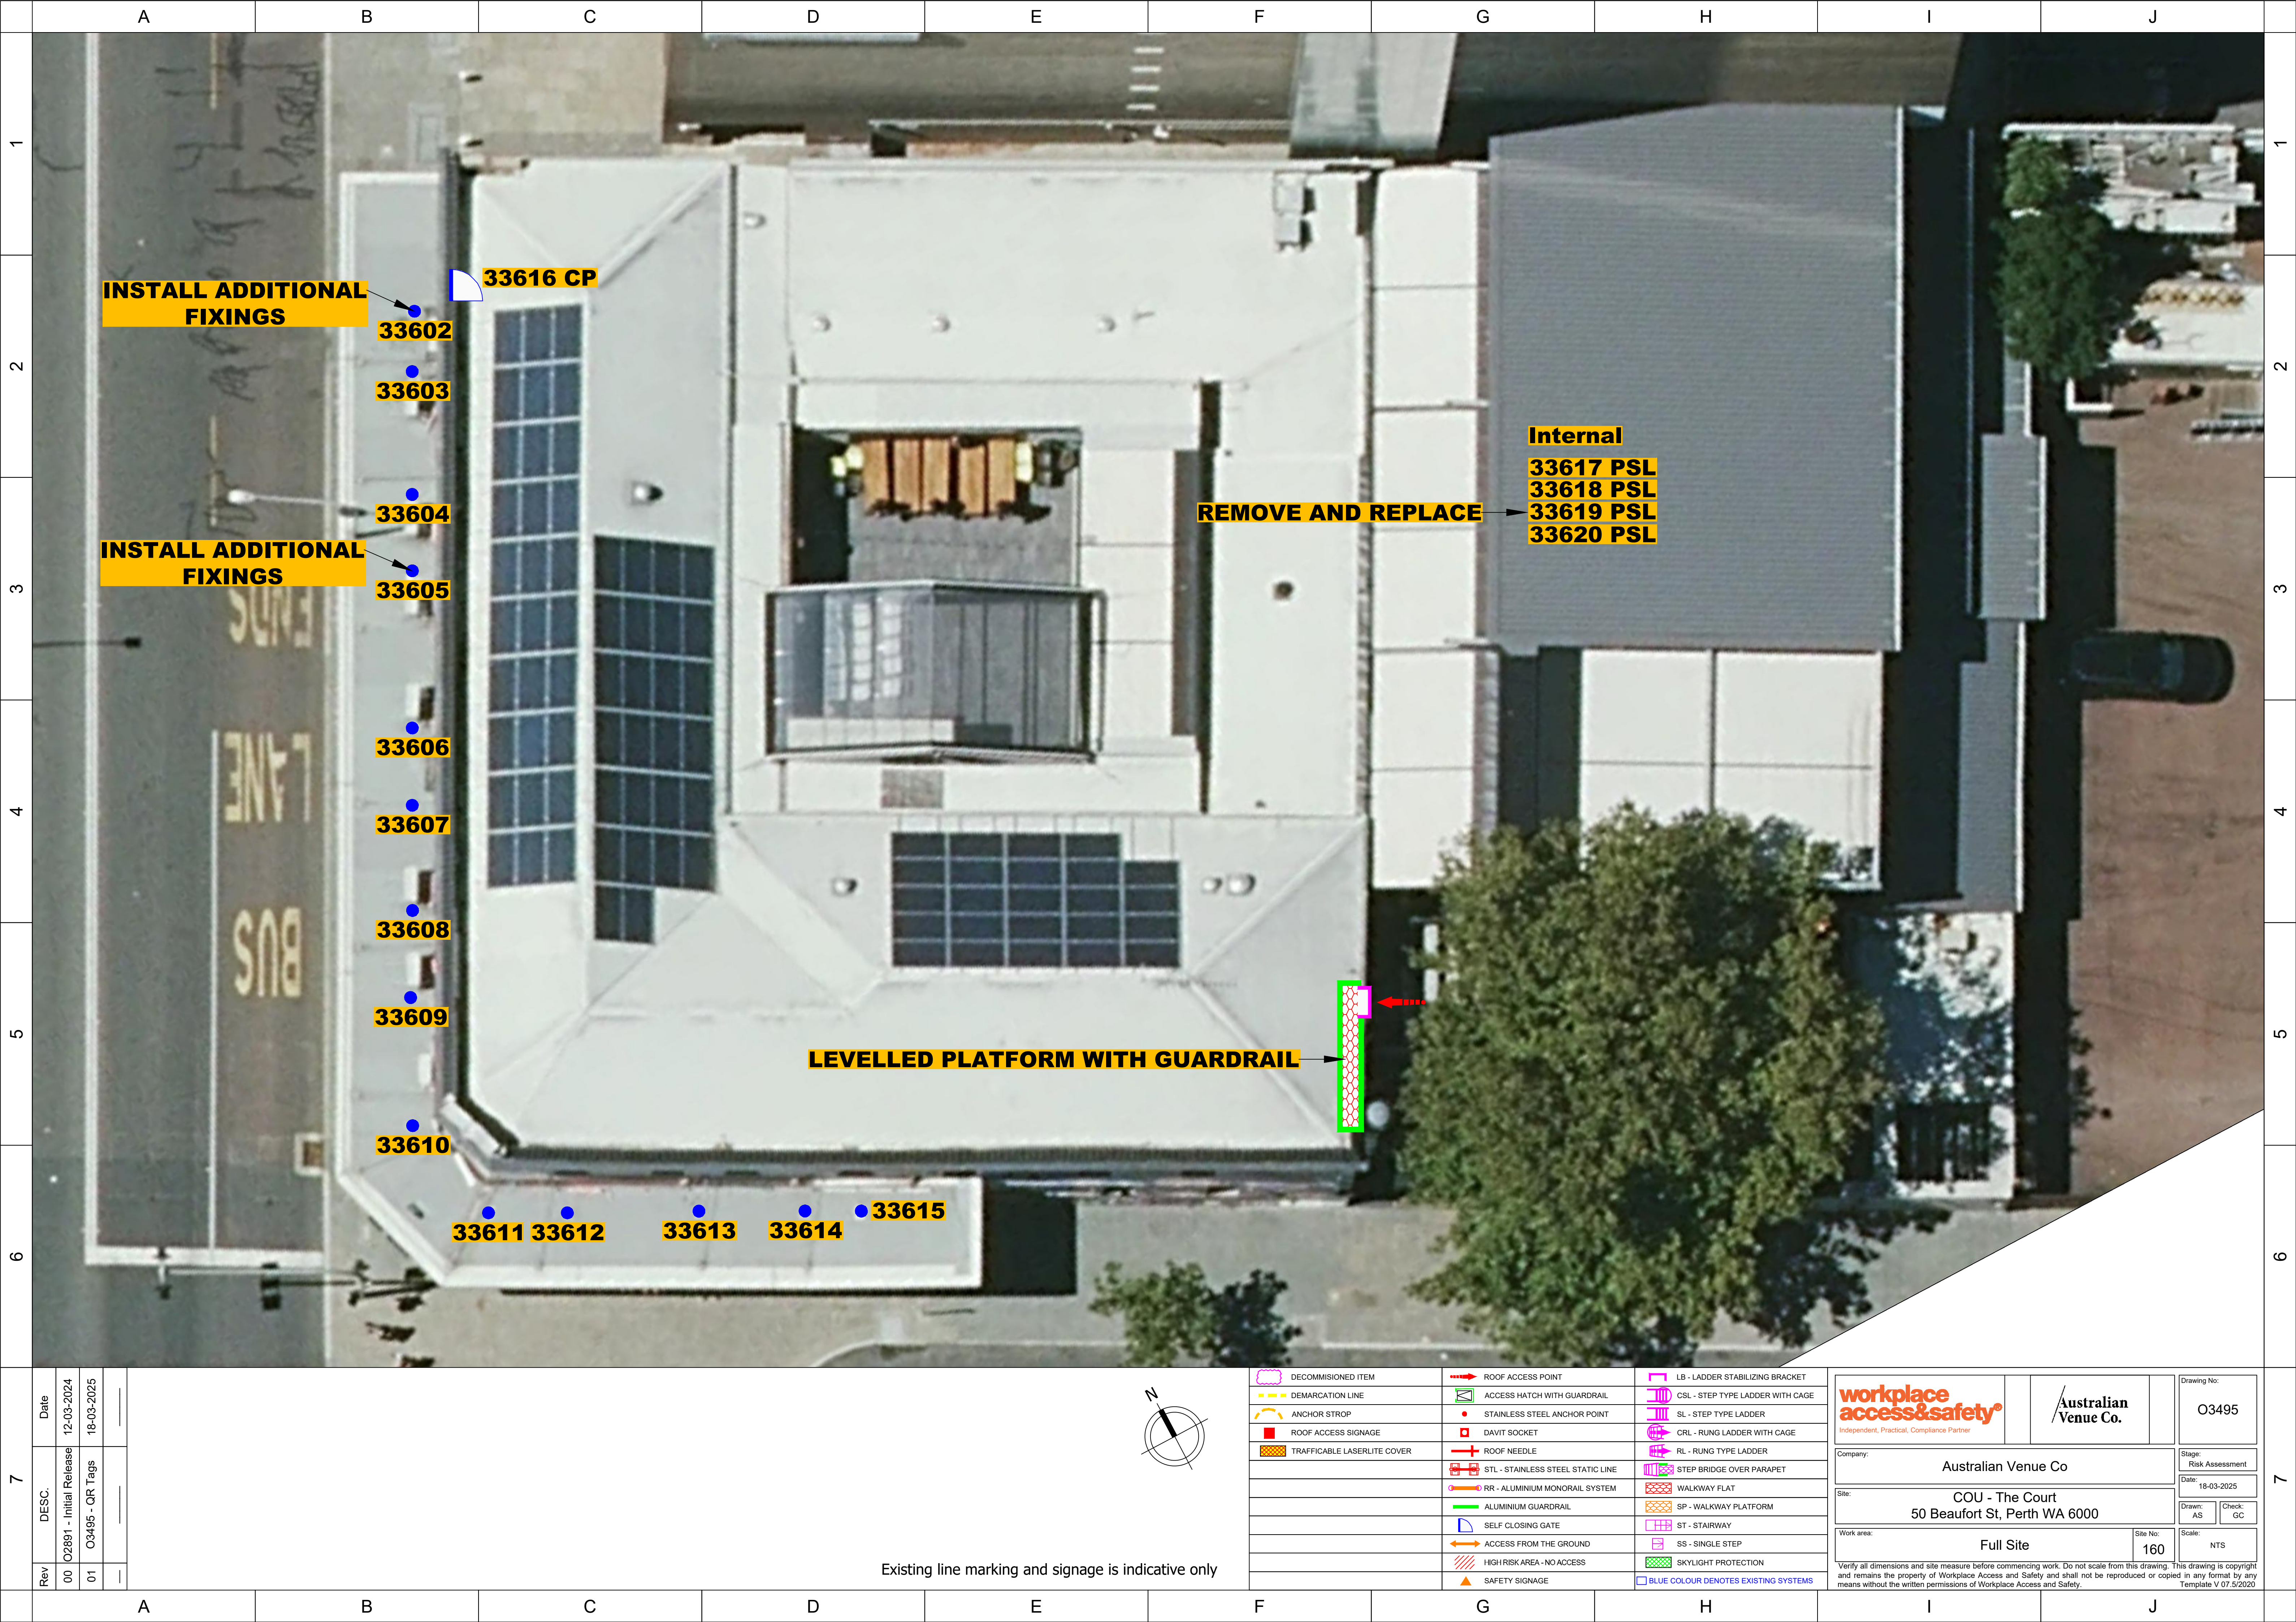

7			
Rev	DESC.	Date	
00	O2891 - Initial Release	12-03-2024	
01	O3495 - QR Tags	18-03-2025	
—	—	—	

Existing line marking and signage is indicative only



	DECOMMISSIONED ITEM		ROOF ACCESS POINT		LB - LADDER STABILIZING BRACKET
	DEMARICATION LINE		ACCESS HATCH WITH GUARDRAIL		CSL - STEP TYPE LADDER WITH CAGE
	ANCHOR STROP		STAINLESS STEEL ANCHOR POINT		SL - STEP TYPE LADDER
	ROOF ACCESS SIGNAGE		DAVIT SOCKET		CRL - RUNG LADDER WITH CAGE
	TRAFFICABLE LASERLITE COVER		ROOF NEEDLE		RL - RUNG TYPE LADDER
			STL - STAINLESS STEEL STATIC LINE		STEP BRIDGE OVER PARAPET
			RR - ALUMINIUM MONORAIL SYSTEM		WALKWAY FLAT
			ALUMINIUM GUARDRAIL		SP - WALKWAY PLATFORM
			SELF CLOSING GATE		ST - STAIRWAY
			ACCESS FROM THE GROUND		SS - SINGLE STEP
			HIGH RISK AREA - NO ACCESS		SKYLIGHT PROTECTION
			SAFETY SIGNAGE		BLUE COLOUR DENOTES EXISTING SYSTEMS

 <i>Independent, Practical, Compliance Partner</i>				Drawing No: O3495	
Company: Australian Venue Co				Stage: Risk Assessment	
Site: COU - The Court 50 Beaufort St, Perth WA 6000				Date: 18-03-2025	
Work area: Full Site				Drawn: AS	
				Check: GC	
Site No: 160				Scale: NTS	
Verify all dimensions and site measure before commencing work. Do not scale from this drawing. This drawing is copyright and remains the property of Workplace Access and Safety and shall not be reproduced or copied in any format by any means without the written permissions of Workplace Access and Safety.					
Template V 07.5/2020					