

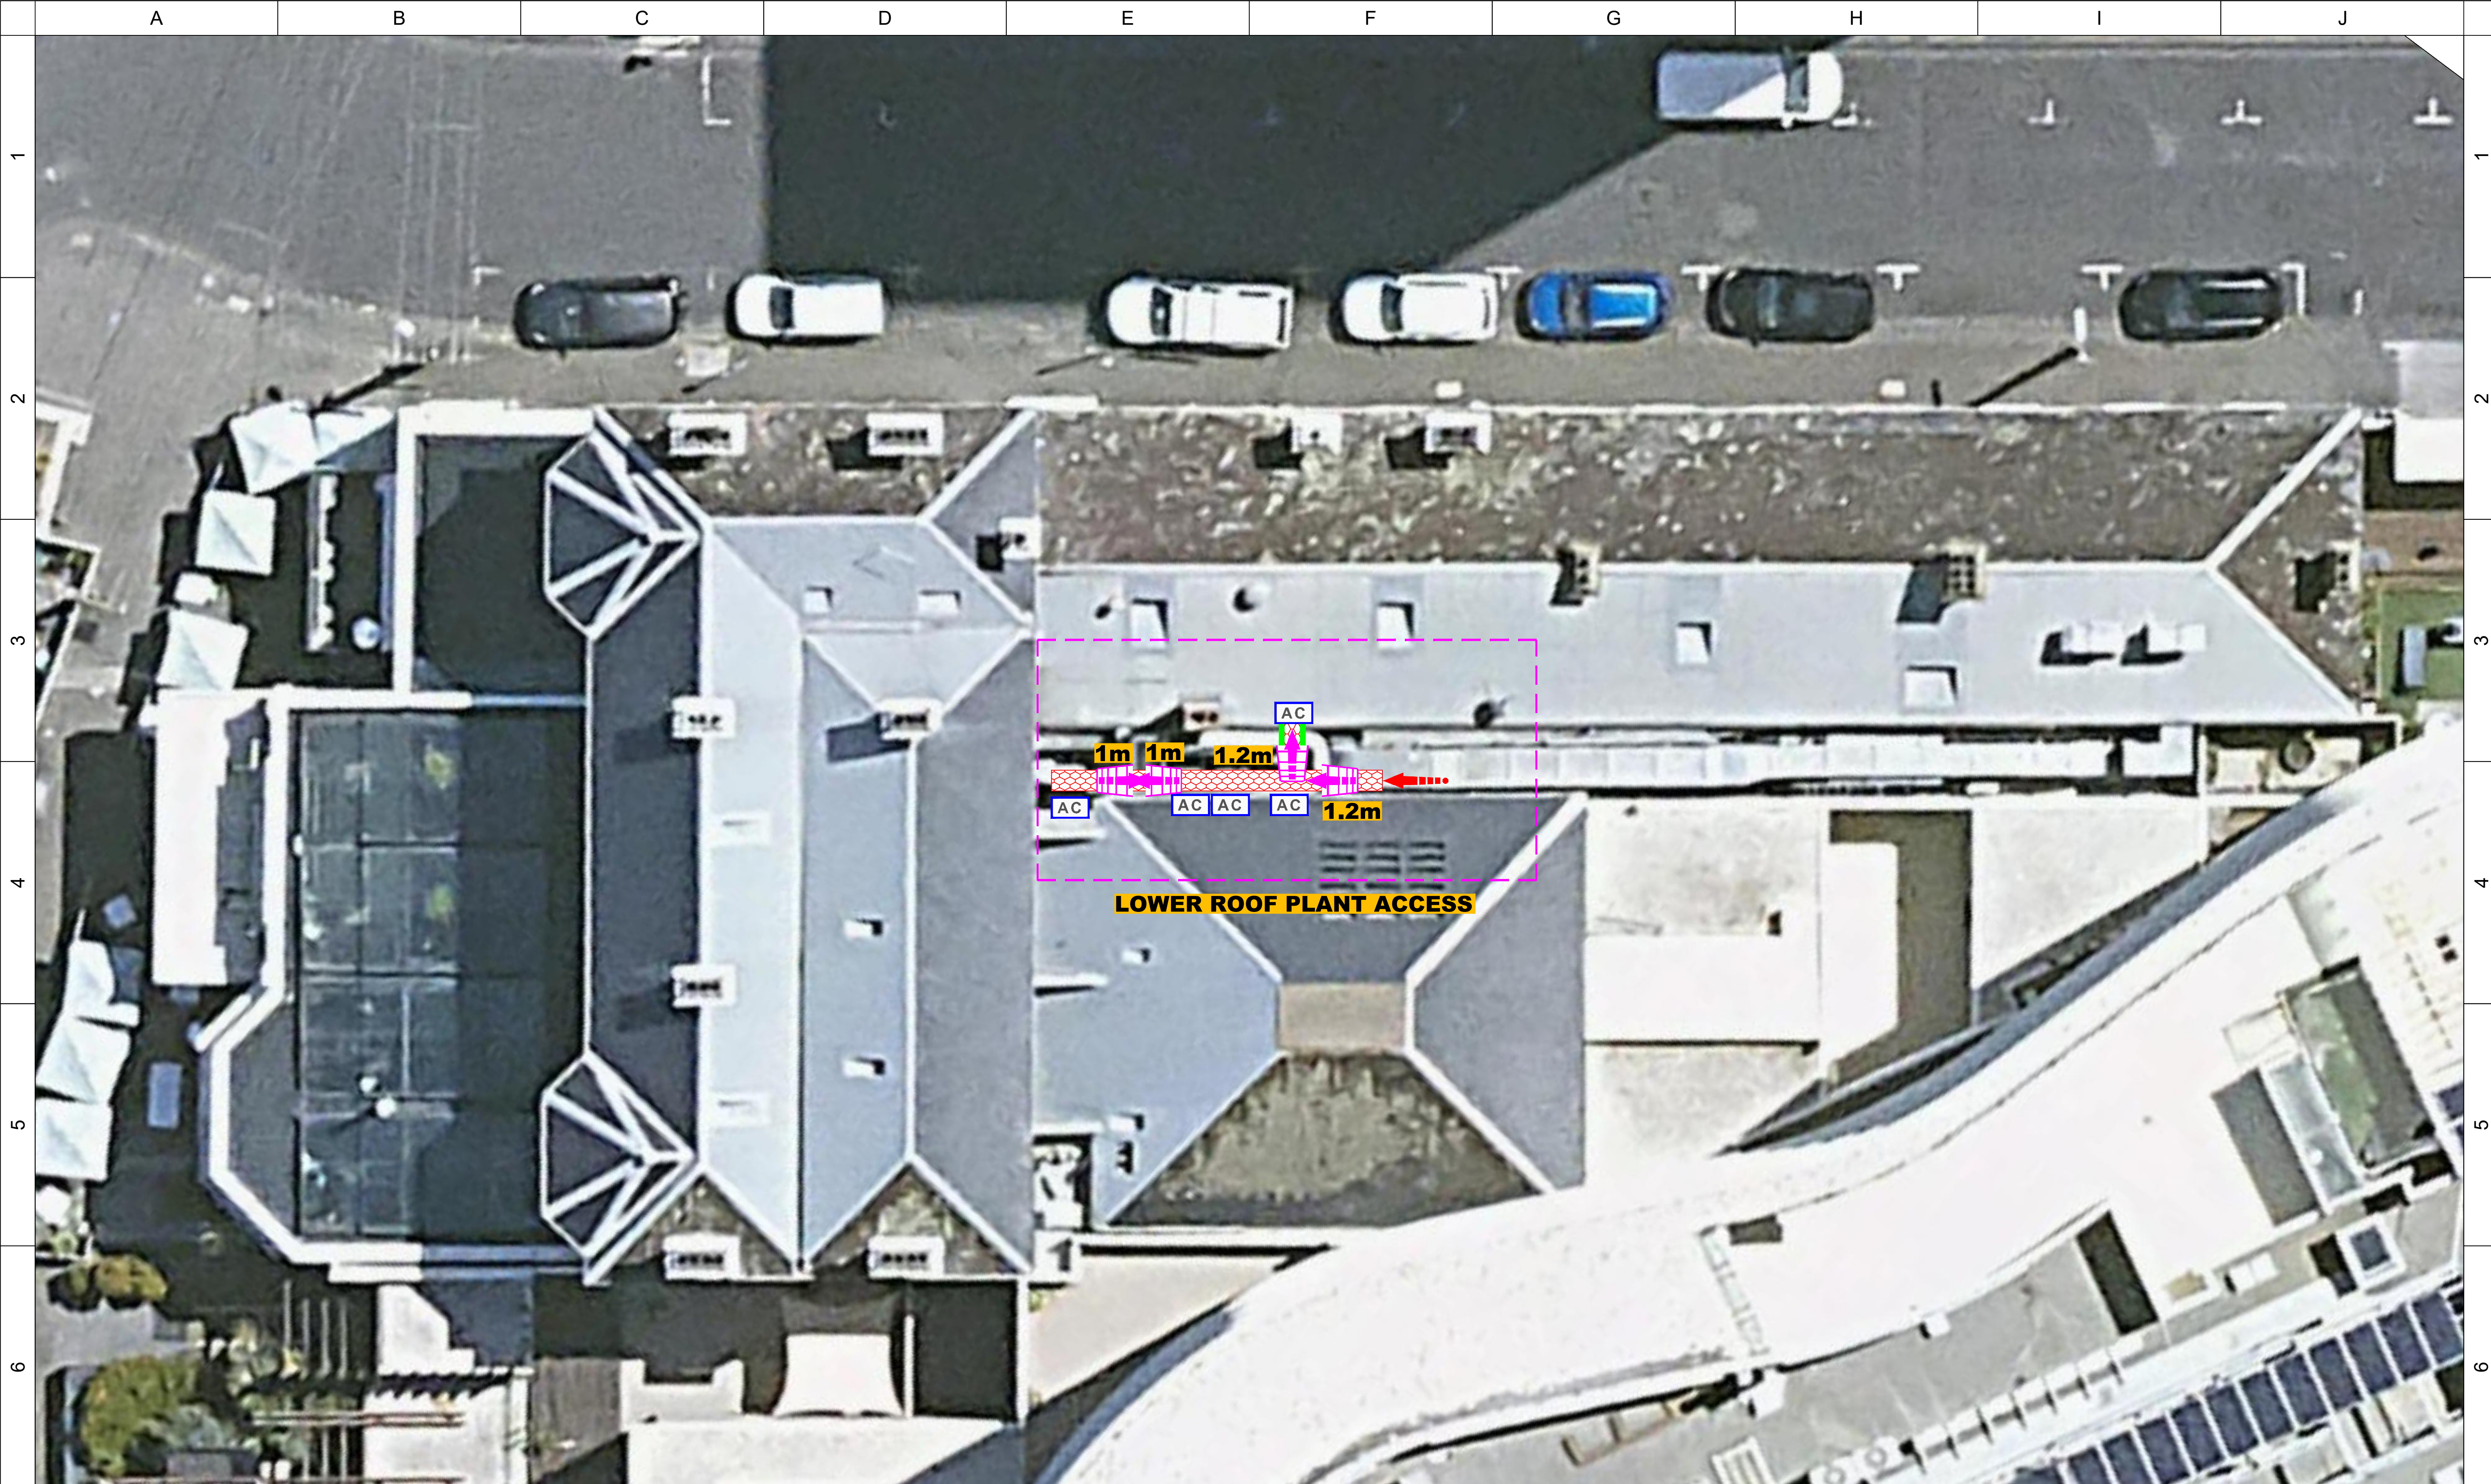


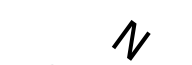

7	Date	28-02-2025		
	DESC.	O3495 - Initial Release		
Rev	00			

 

Existing line marking and signage is indicative only

 DECOMMISSIONED ITEM	 ROOF ACCESS POINT	 LB - LADDER STABILIZING BRACKET
 DEMARCATION LINE	 ACCESS HATCH WITH GUARDRAIL	 CSL - STEP TYPE LADDER WITH CAGE
 ANCHOR STROP	 STAINLESS STEEL ANCHOR POINT	 SL - STEP TYPE LADDER
 ROOF ACCESS SIGNAGE	 DAVIT SOCKET	 CRL - RUNG LADDER WITH CAGE
 TRAFFICABLE LASERLITE COVER	 ROOF NEEDLE	 RL - RUNG TYPE LADDER
	 STL - STAINLESS STEEL STATIC LINE	 STEP BRIDGE OVER PARAPET
	 RR - ALUMINIUM MONORAIL SYSTEM	 WALKWAY FLAT
	 SP - WALKWAY GUARDRAIL	 SP - WALKWAY PLATFORM
	 SELF CLOSING GATE	 ST - STAIRWAY
	 ACCESS FROM THE GROUND	 SS - SINGLE STEP
	 HIGH RISK AREA - NO ACCESS	 SKYLIGHT PROTECTION
	 SAFETY SIGNAGE	 BLUE COLOUR DENOTES EXISTING SYSTEMS

				Drawing No: O3495
Company: Australian Venue Co.				Stage: Risk Assessment
Site: ESP - Hotel Esplanade 11 The Esplanade, St Kilda VIC 3182				Date: 28-02-2025
Work area: Main Building		Site No: 	Drawn: AS	Check: GC
Scale: NTS				

Verify all dimensions and site measure before commencing work. Do not scale from this drawing. This drawing is copyright and remains the property of Workplace Access and Safety and shall not be reproduced or copied in any format by any means without the written permission of Workplace Access and Safety.

Template V 07.5/2020