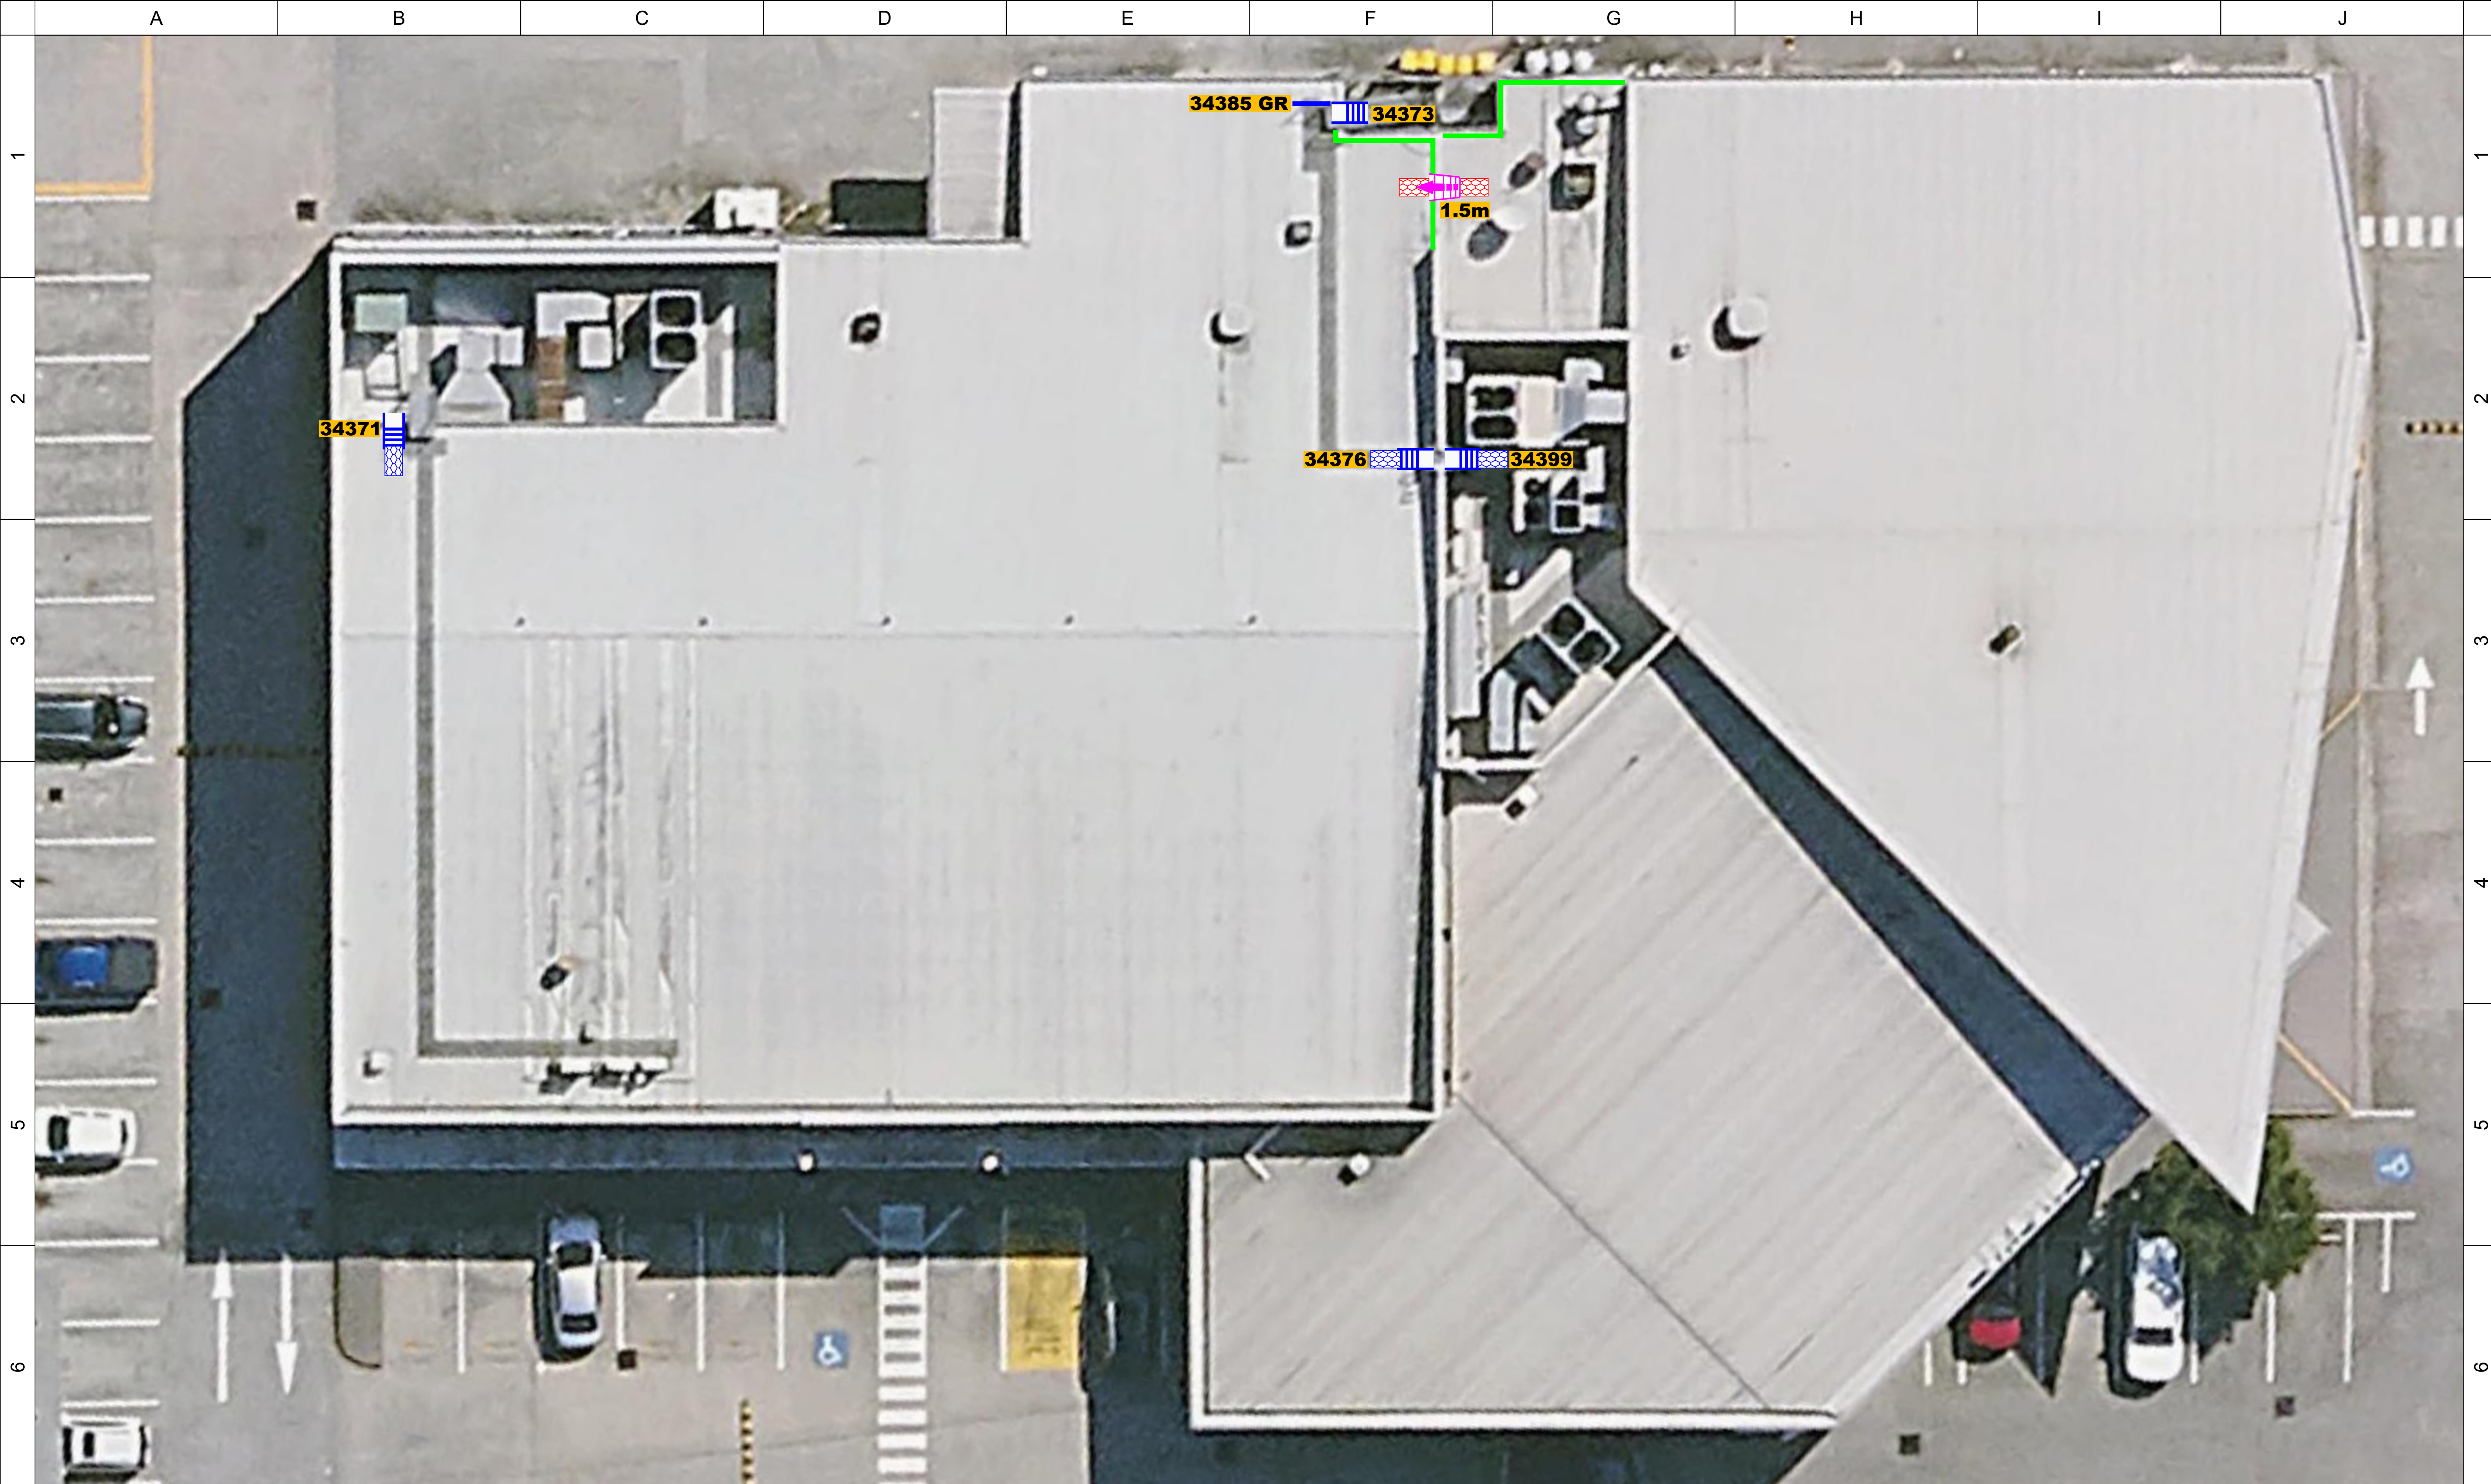


Existing line marking and signage is indicative only

	DECOMMISSIONED ITEM		ROOF ACCESS POINT		LB - LADDER STABILIZING BRACKET
	DEMARICATION LINE		ACCESS HATCH WITH GUARDRAIL		CSL - STEP TYPE LADDER WITH CAGE
	ANCHOR STROP		STAINLESS STEEL ANCHOR POINT		SL - STEP TYPE LADDER
	ROOF ACCESS SIGNAGE		DAVIT SOCKET		CLR - RUNG LADDER WITH CAGE
	TRAFFICABLE LASERLITE COVER		ROOF NEEDLE		RL - RUNG TYPE LADDER
			STL - STAINLESS STEEL STATIC LINE		STEP BRIDGE OVER PARAPET
			RR - ALUMINIUM MONORAIL SYSTEM		WALKWAY FLAT
			ALUMINIUM GUARDRAIL		SP - WALKWAY PLATFORM
			SELF CLOSING GATE		ST - STAIRWAY
			ACCESS FROM THE GROUND		SS - SINGLE STEP
			HIGH RISK AREA - NO ACCESS		SKYLIGHT PROTECTION
			SAFETY SIGNAGE		BLUE COLOUR DENOTES EXISTING SYSTEMS

		Drawing No: O3495
		Independent, Practical, Compliance Partner
Company: Australian Venue Co.		Stage: Risk Assessment
Site: JVOXL - The Ox (Oxley Hotel) Cnr Ipswich &, Oxley Rd, Oxley QLD 4075		Date: 26-02-2025
Work area: Main Building	Site No: _____	Drawn: AS Check: GC Scale: NTS
Verify all dimensions and site measure before commencing work. Do not scale from this drawing. This drawing is copyright and remains the property of Workplace Access and Safety and shall not be reproduced or copied in any format by any person without the written permission of Workplace Access and Safety.		