


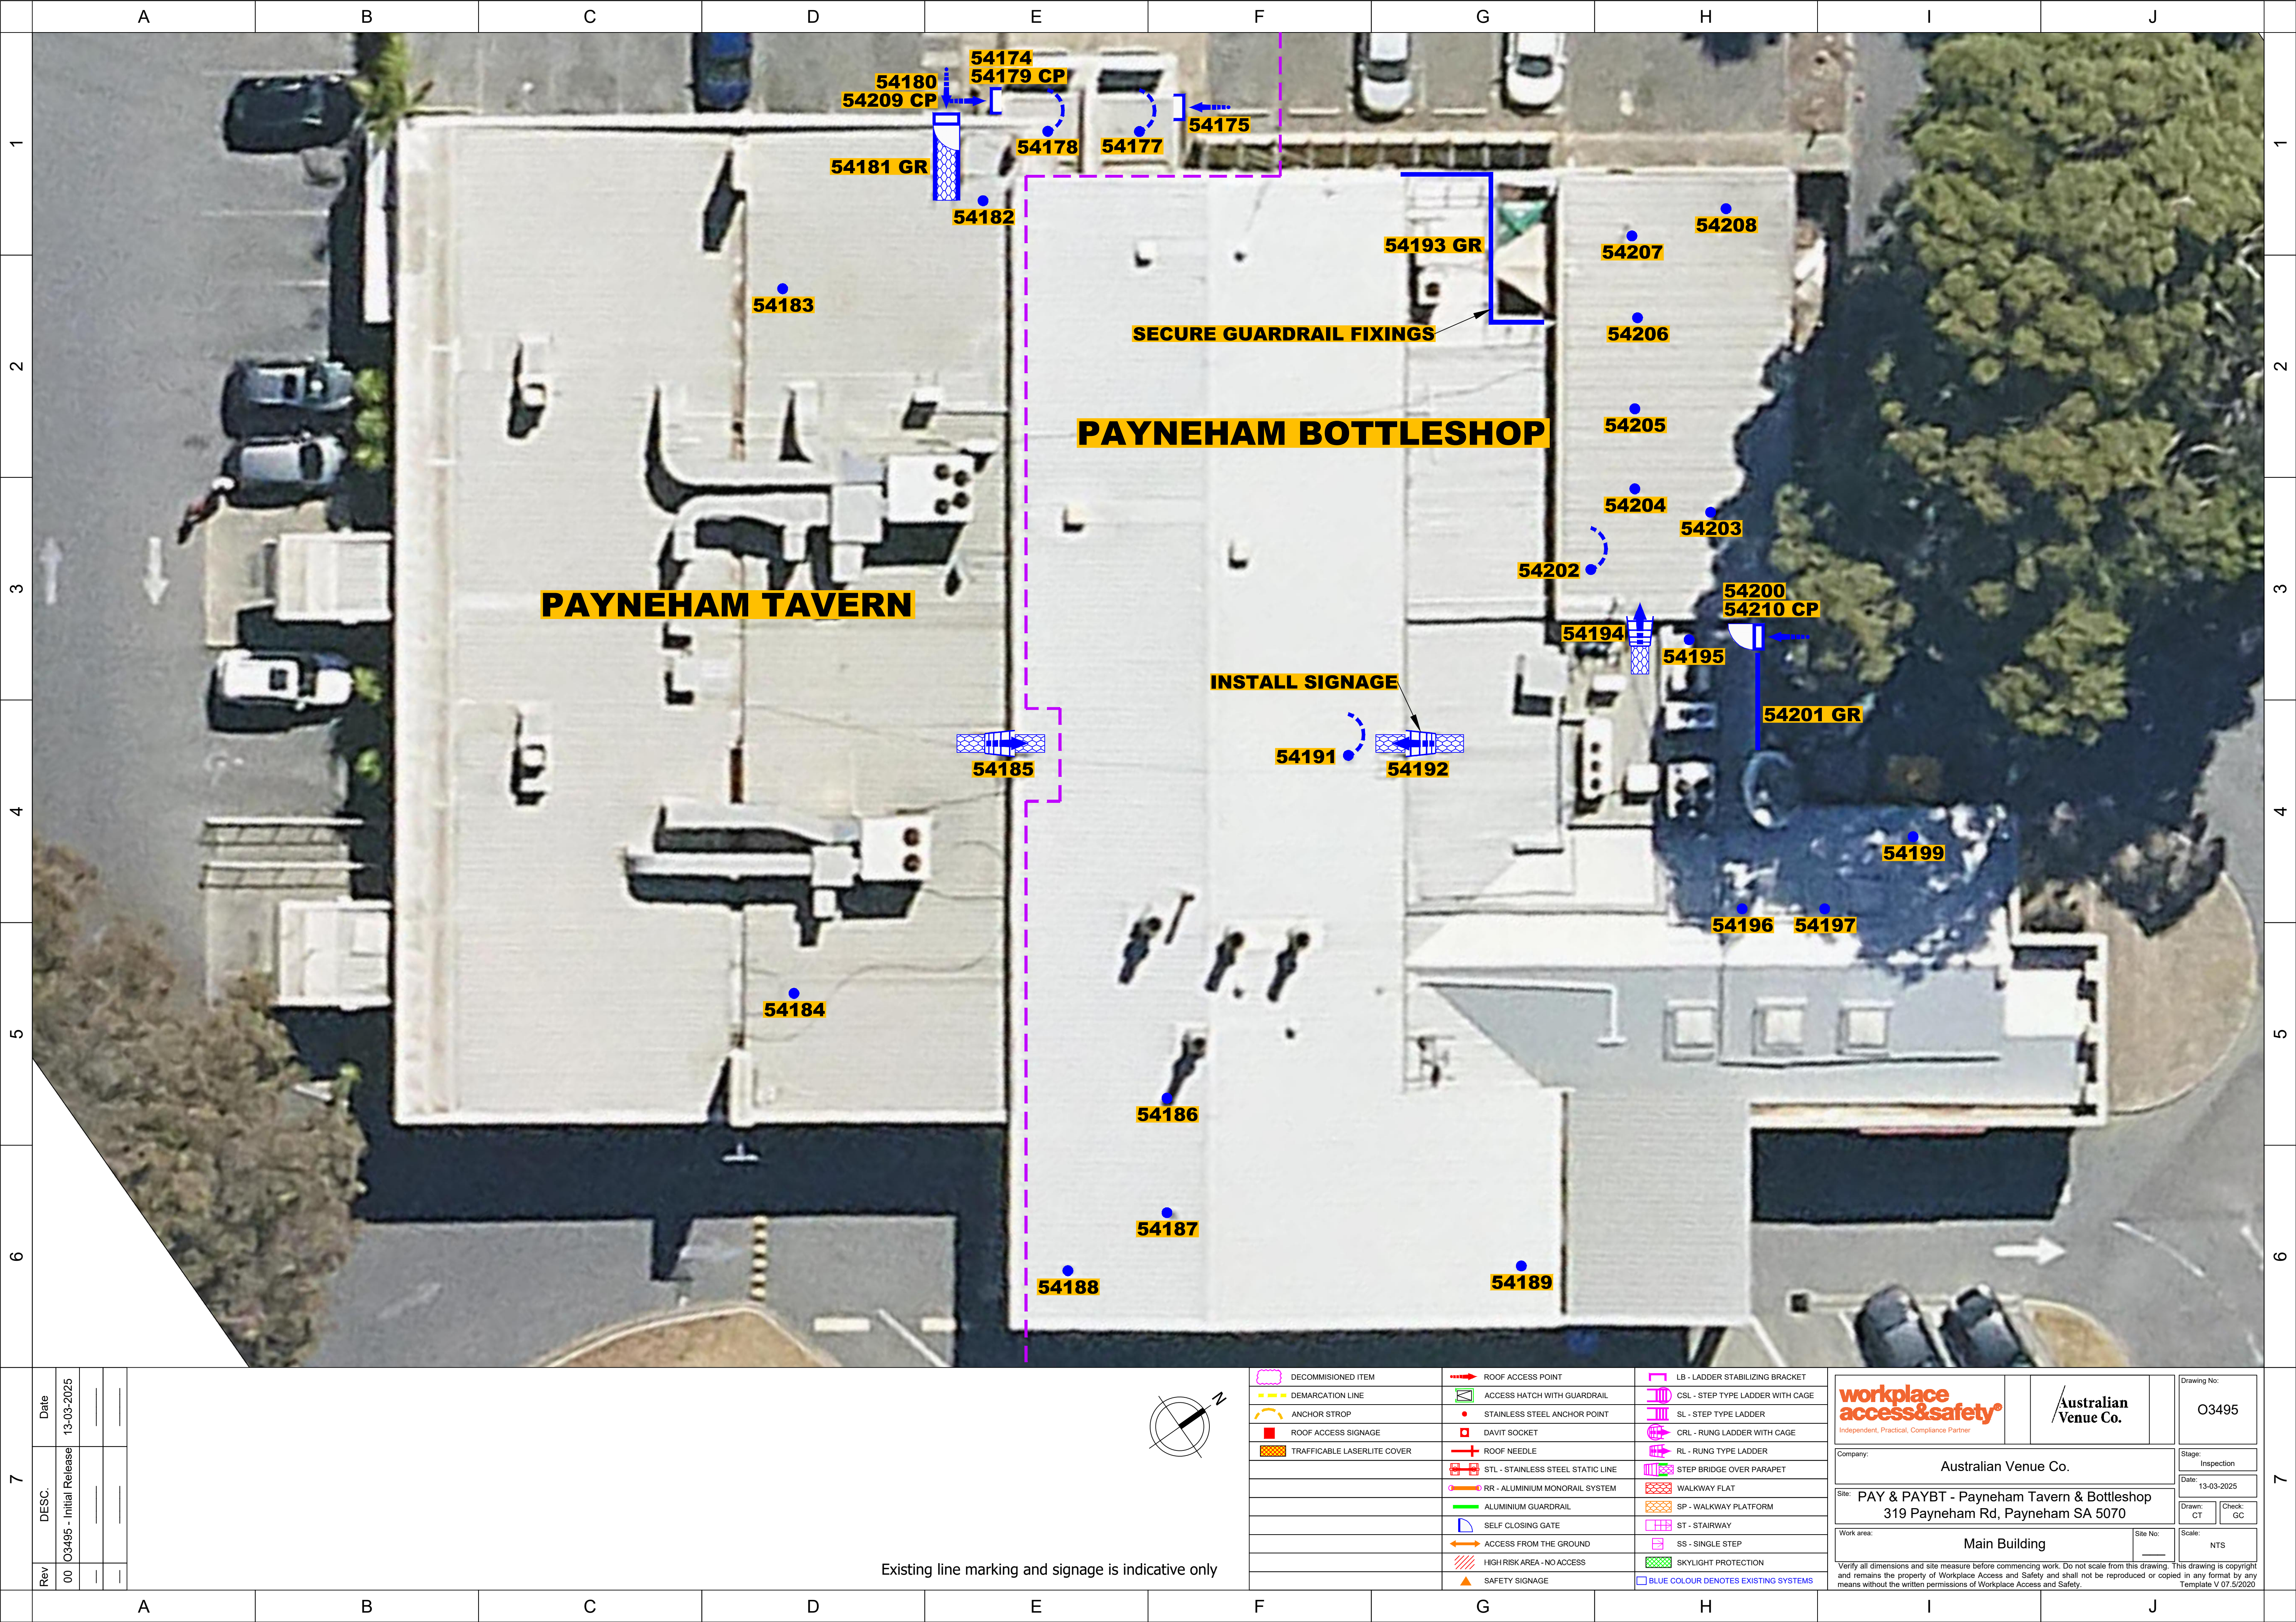

Rev	DESC.	Date
00	03495 - Initial Release	13-03-2025

Existing line marking and signage is indicative only

	DECOMMISSIONED ITEM		ROOF ACCESS POINT		LB - LADDER STABILIZING BRACKET
	DEMARICATION LINE		ACCESS HATCH WITH GUARDRAIL		CSL - STEP TYPE LADDER WITH CAGE
	ANCHOR STROP		STAINLESS STEEL ANCHOR POINT		SL - STEP TYPE LADDER
	ROOF ACCESS SIGNAGE		DAVIT SOCKET		CRL - RUNG LADDER WITH CAGE
	TRAFFICABLE LASERLITE COVER		ROOF NEEDLE		RL - RUNG TYPE LADDER
			STL - STAINLESS STEEL STATIC LINE		STEP BRIDGE OVER PARAPET
			RR - ALUMINIUM MONORAIL SYSTEM		WALKWAY FLAT
			ALUMINIUM GUARDRAIL		SP - WALKWAY PLATFORM
			SELF CLOSING GATE		ST - STAIRWAY
			ACCESS FROM THE GROUND		SS - SINGLE STEP
			HIGH RISK AREA - NO ACCESS		SKYLIGHT PROTECTION
			SAFETY SIGNAGE		BLUE COLOUR DENOTES EXISTING SYSTEMS

		Drawing No: O3495
Company: Australian Venue Co.		Stage: Inspection
Site: PAY & PAYBT - Payneham Tavern & Bottleshop 319 Payneham Rd, Payneham SA 5070		Date: 13-03-2025
Work area: Main Building		Drawn: CT Check: GC
Site No: _____		Scale: NTS
Verify all dimensions and site measure before commencing work. Do not scale from this drawing. This drawing is copyright and remains the property of Workplace Access and Safety and shall not be reproduced or copied in any format by any means without the written permissions of Workplace Access and Safety. Template V 07.5/2020		