


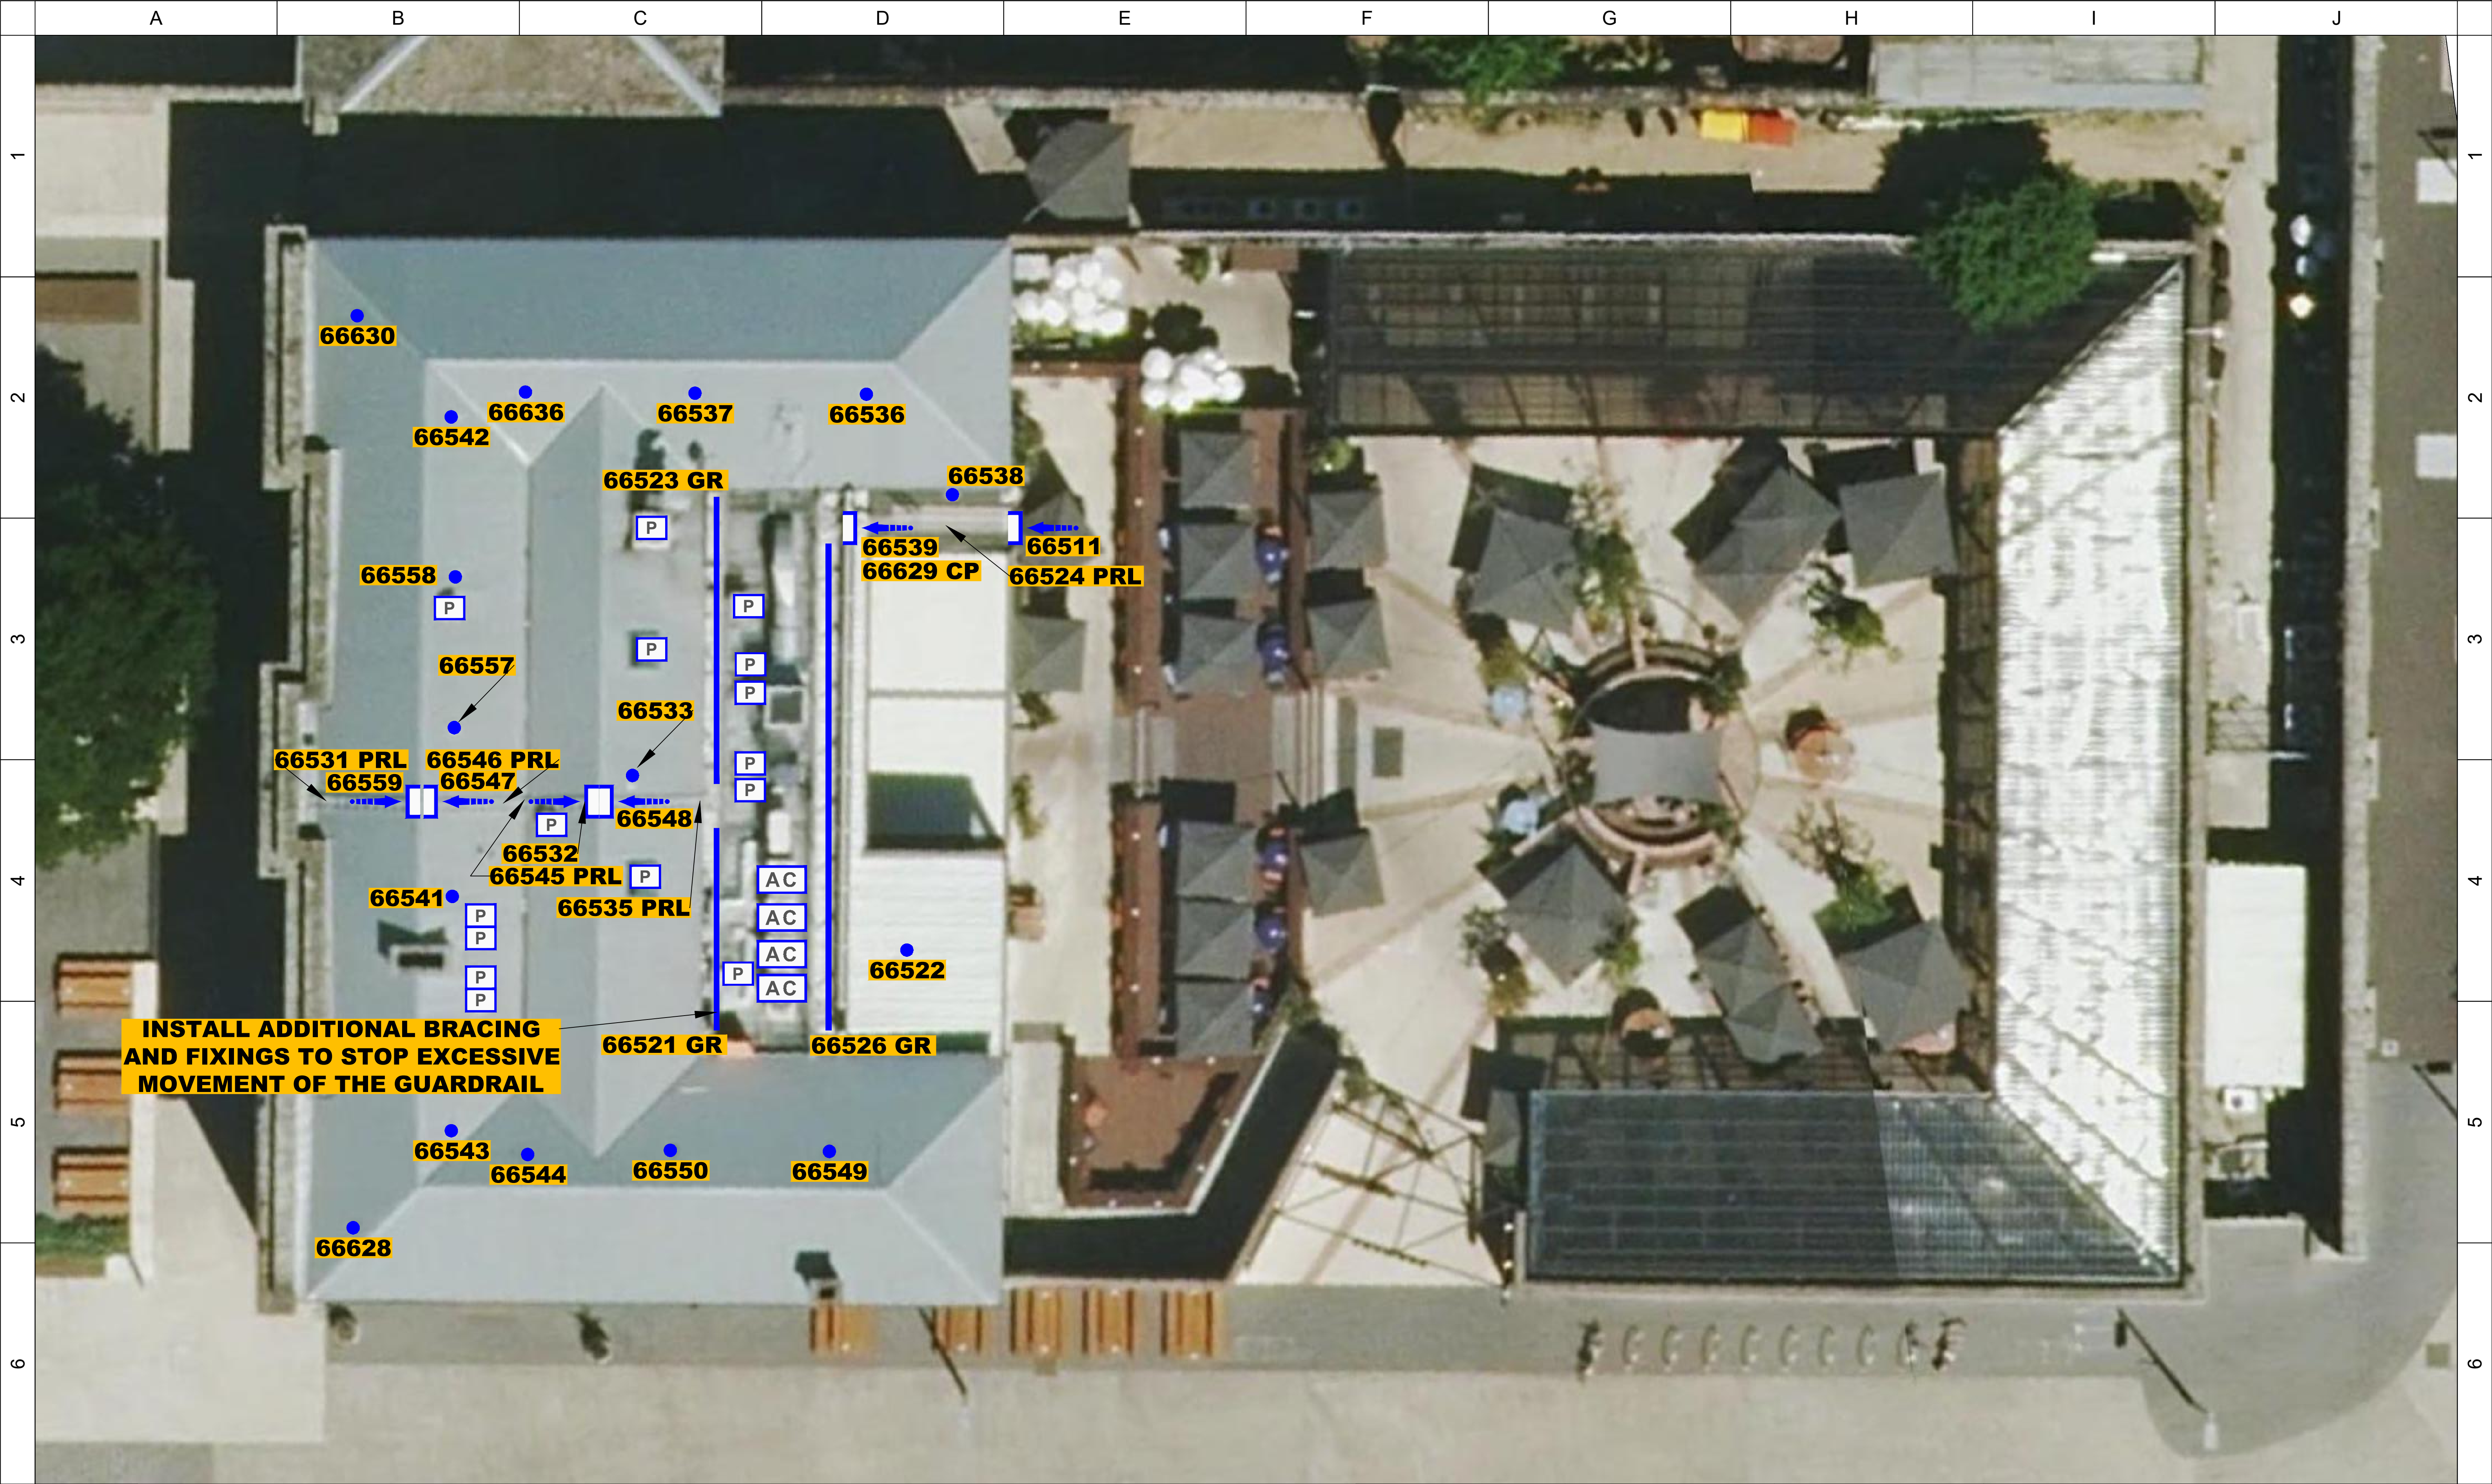

Rev	DESC.	Date	
		00	03495 - Initial Release

Existing line marking and signage is indicative only

	DECOMMISSIONED ITEM		ROOF ACCESS POINT		LB - LADDER STABILIZING BRACKET
	DEMARICATION LINE		ACCESS HATCH WITH GUARDRAIL		CSL - STEP TYPE LADDER WITH CAGE
	ANCHOR STROP		STAINLESS STEEL ANCHOR POINT		SL - STEP TYPE LADDER
	ROOF ACCESS SIGNAGE		DAVIT SOCKET		CRL - RUNG LADDER WITH CAGE
	TRAFFICABLE LASERLITE COVER		ROOF NEEDLE		RL - RUNG TYPE LADDER
			STL - STAINLESS STEEL STATIC LINE		SP - WALKWAY PLATFORM
			RR - ALUMINIUM MONORAIL SYSTEM		WALKWAY FLAT
			ALUMINIUM GUARDRAIL		ST - STAIRWAY
			SELF CLOSING GATE		SS - SINGLE STEP
			ACCESS FROM THE GROUND		SKYLIGHT PROTECTION
			HIGH RISK AREA - NO ACCESS		BLUE COLOUR DENOTES EXISTING SYSTEMS
			SAFETY SIGNAGE		

Independent, Practical, Compliance Partner

Company:
Australian Venue Co.

Site:
PEN - BrewDog Pentridge Prisons
2 Anglers Way, Maribyrnong VIC 3032

Work area:
Main Building

Drawing No:
O3495

Stage:
Risk Assessment

Date:
20-02-2025

Drawn:
AS

Check:
GC

Scale:
NTS

Verify all dimensions and site measure before commencing work. Do not scale from this drawing. This drawing is copyright and remains the property of Workplace Access and Safety and shall not be reproduced or copied in any format by any means without the written permissions of Workplace Access and Safety.
Template V 07.5/2020