


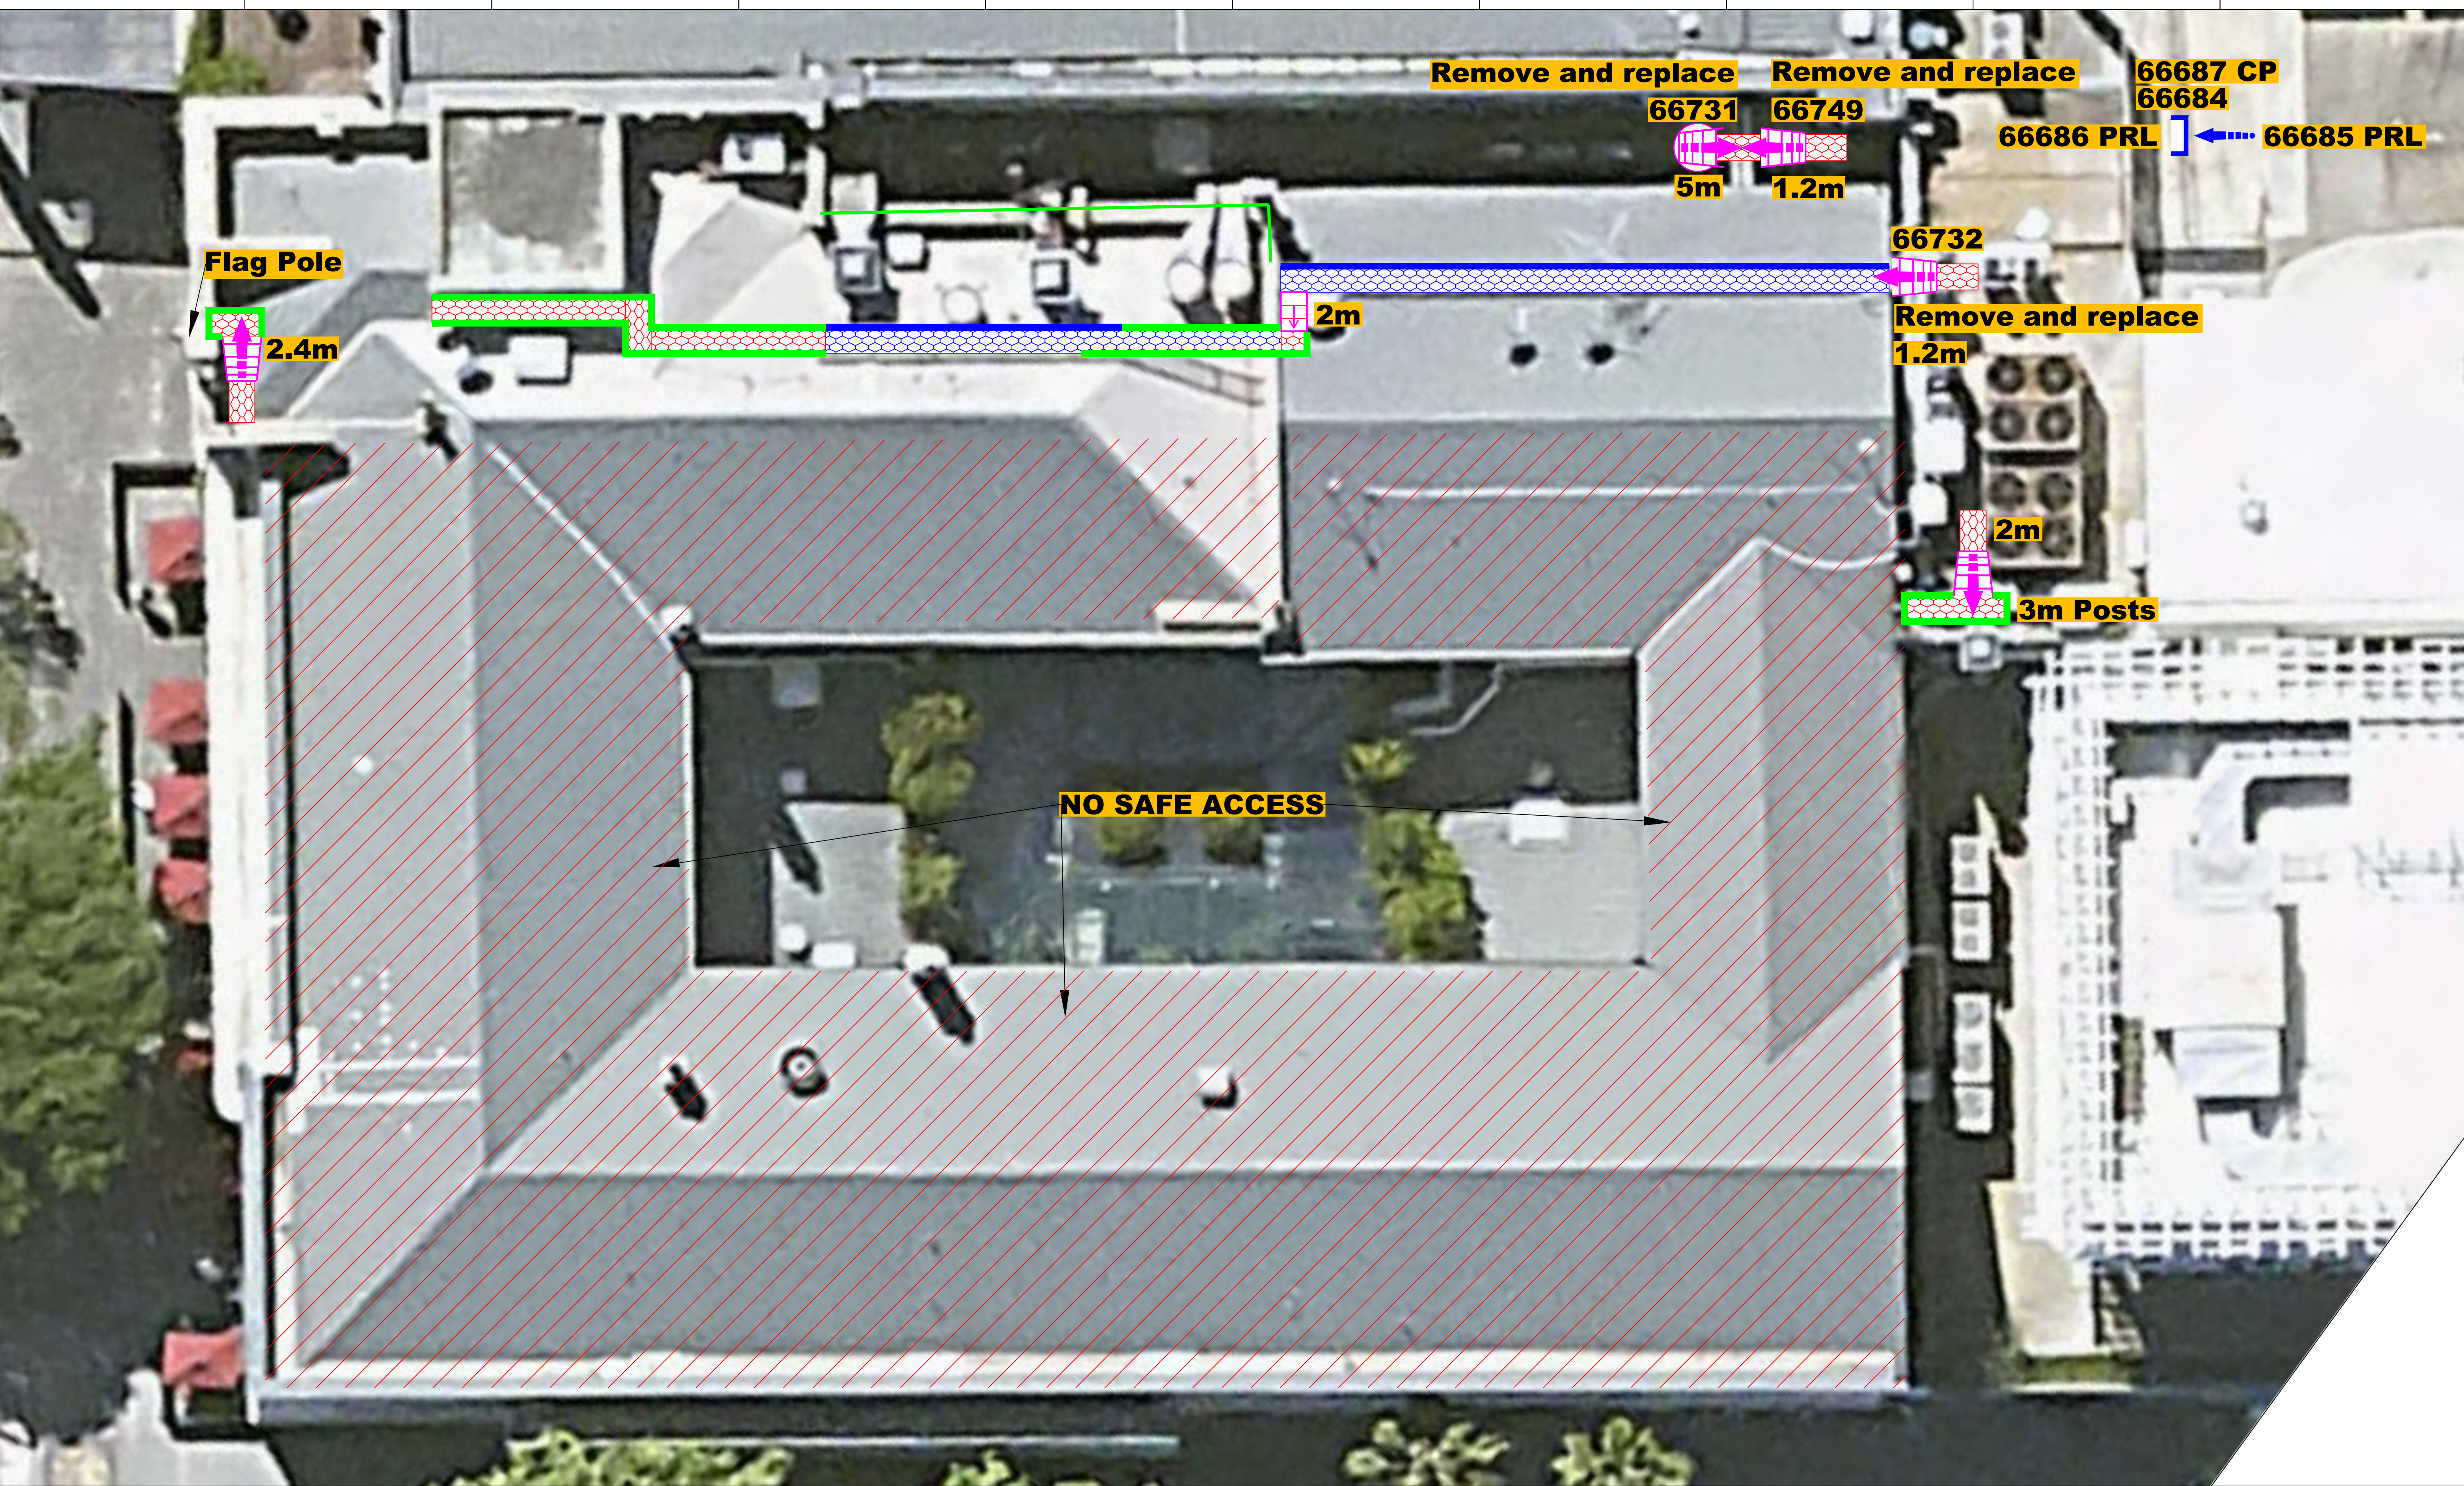

Rev	DESC.	Date
00	03495 - Initial Release	28-02-2025

DECOMMISSIONED ITEM	ROOF ACCESS POINT	LB - LADDER STABILIZING BRACKET
DEMARCATION LINE	ACCESS HATCH WITH GUARDRAIL	CSL - STEP TYPE LADDER WITH CAGE
ANCHOR STROP	STAINLESS STEEL ANCHOR POINT	SL - STEP TYPE LADDER
ROOF ACCESS SIGNAGE	DAVIT SOCKET	CRL - RUNG LADDER WITH CAGE
TRAFFICABLE LASERLITE COVER	ROOF NEEDLE	RL - RUNG TYPE LADDER
	STL - STAINLESS STEEL STATIC LINE	STEP BRIDGE OVER PARAPET
	RR - ALUMINIUM MONORAIL SYSTEM	WALKWAY FLAT
	ALUMINIUM GUARDRAIL	SP - WALKWAY PLATFORM
	SELF CLOSING GATE	ST - STAIRWAY
	ACCESS FROM THE GROUND	SS - SINGLE STEP
	HIGH RISK AREA - NO ACCESS	SKYLIGHT PROTECTION
	SAFETY SIGNAGE	BLUE COLOUR DENOTES EXISTING SYSTEMS

Independent, Practical, Compliance Partner

Drawing No:
O3495

Stage:
Risk Assessment

Date:
28/02/2025

Drawn:
AS

Check:
GC

Company:
Australian Venue Co.

Site:
**PRI - The Prince of Wales Hotel
2 Acland St, St Kilda VIC 3182**

Work area:
Main Building

Site No:

Scale:
NTS

Verify all dimensions and site measure before commencing work. Do not scale from this drawing. This drawing is copyright and remains the property of Workplace Access and Safety and shall not be reproduced or copied in any format by any means without the written permissions of Workplace Access and Safety.
Template V 07.5/2020

Existing line marking and signage is indicative only