




7	Date	28-02-2025		
	DESC.	O3495 - Initial Release		
Rev	00			

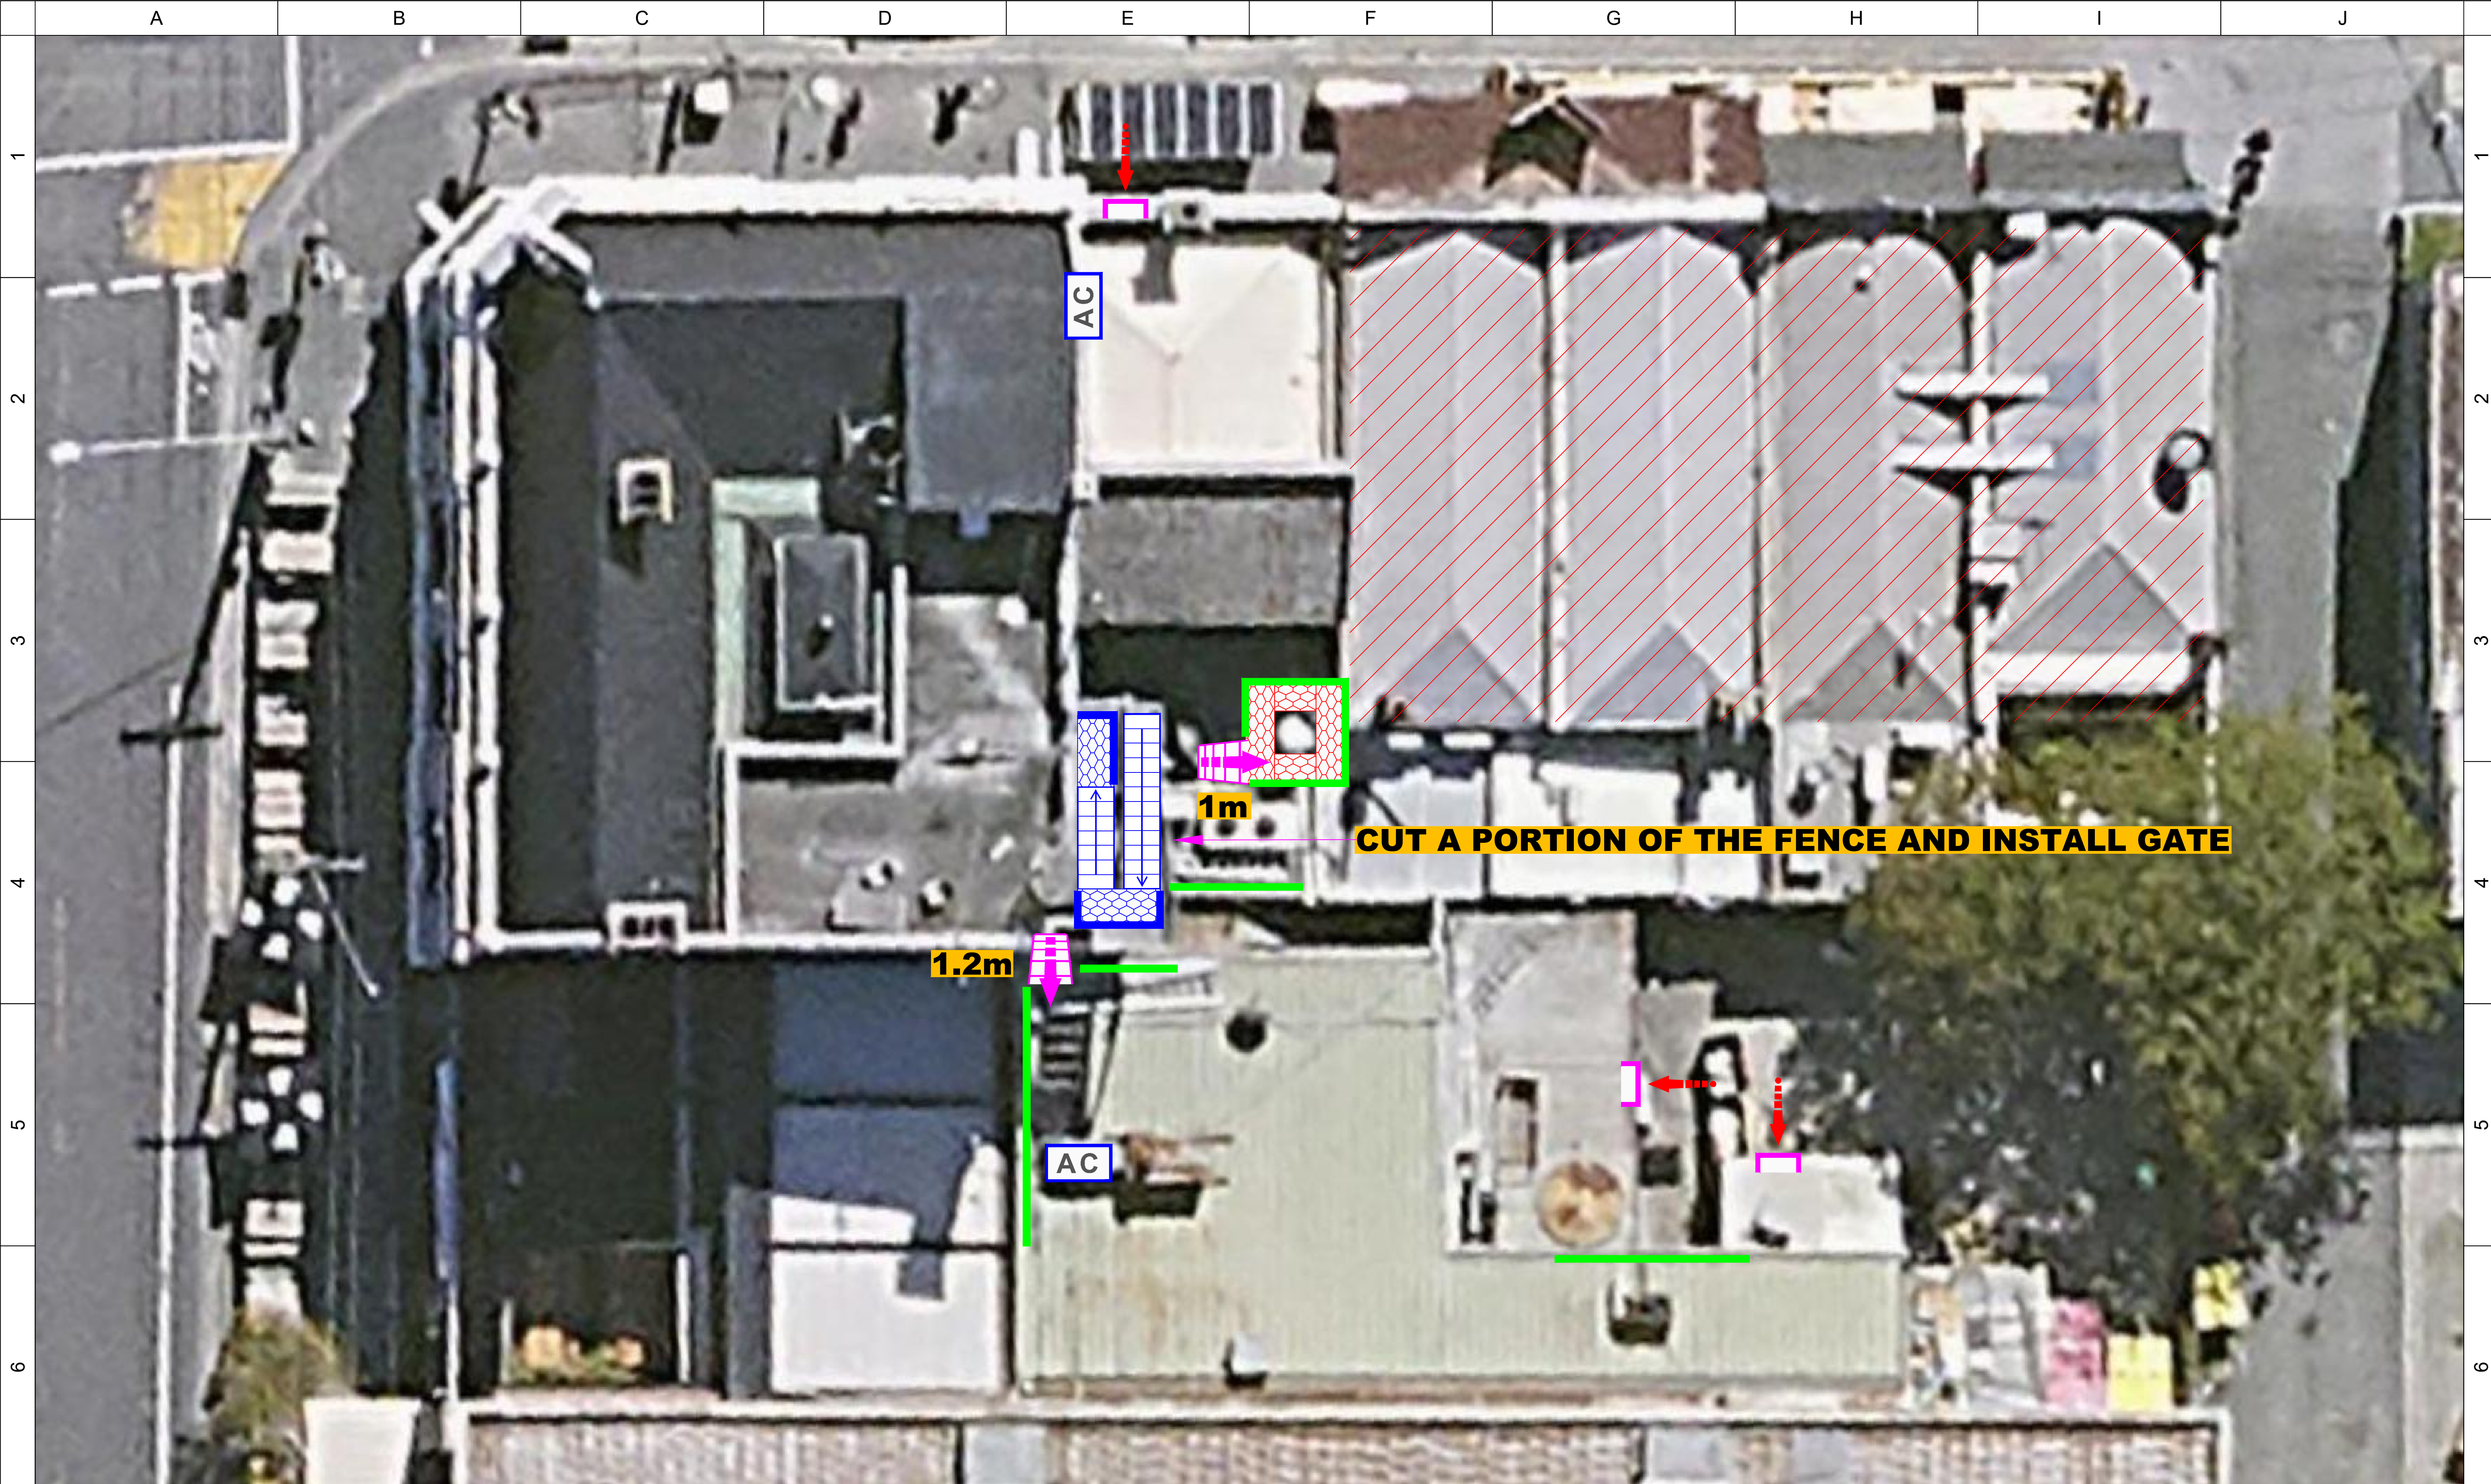

Existing line marking and signage is indicative only

DECOMMISSIONED ITEM	ROOF ACCESS POINT	LB - LADDER STABILIZING BRACKET
DEMARCATION LINE	ACCESS HATCH WITH GUARDRAIL	CSL - STEP TYPE LADDER WITH CAGE
ANCHOR STROP	STAINLESS STEEL ANCHOR POINT	SL - STEP TYPE LADDER
ROOF ACCESS SIGNAGE	DAVIT SOCKET	CRL - RUNG LADDER WITH CAGE
TRAFFICABLE LASERLITE COVER	ROOF NEEDLE	RL - RUNG TYPE LADDER
	STL - STAINLESS STEEL STATIC LINE	STEP BRIDGE OVER PARAPET
	RR - ALUMINIUM MONORAIL SYSTEM	WALKWAY FLAT
	ALUMINIUM GUARDRAIL	SP - WALKWAY PLATFORM
	SELF CLOSING GATE	ST - STAIRWAY
	ACCESS FROM THE GROUND	SS - SINGLE STEP
	HIGH RISK AREA - NO ACCESS	SKYLIGHT PROTECTION
SAFETY SIGNAGE		BLUE COLOUR DENOTES EXISTING SYSTEMS

				Drawing No: O3495
Company: Australian Venue Co.				Stage: Risk Assessment
Site: SWA - Swan Hotel 425 Church St, Richmond VIC 3121				Date: 28/02/2025
Work area: Main Building		Site No: _____	Drawn: AS	Check: GC
Scale: NTS			Verify all dimensions and site measure before commencing work. Do not scale from this drawing. This drawing is copyright and remains the property of Workplace Access and Safety and shall not be reproduced or copied in any format by any means without the written permission of Workplace Access and Safety. Template V 07.5/2020	