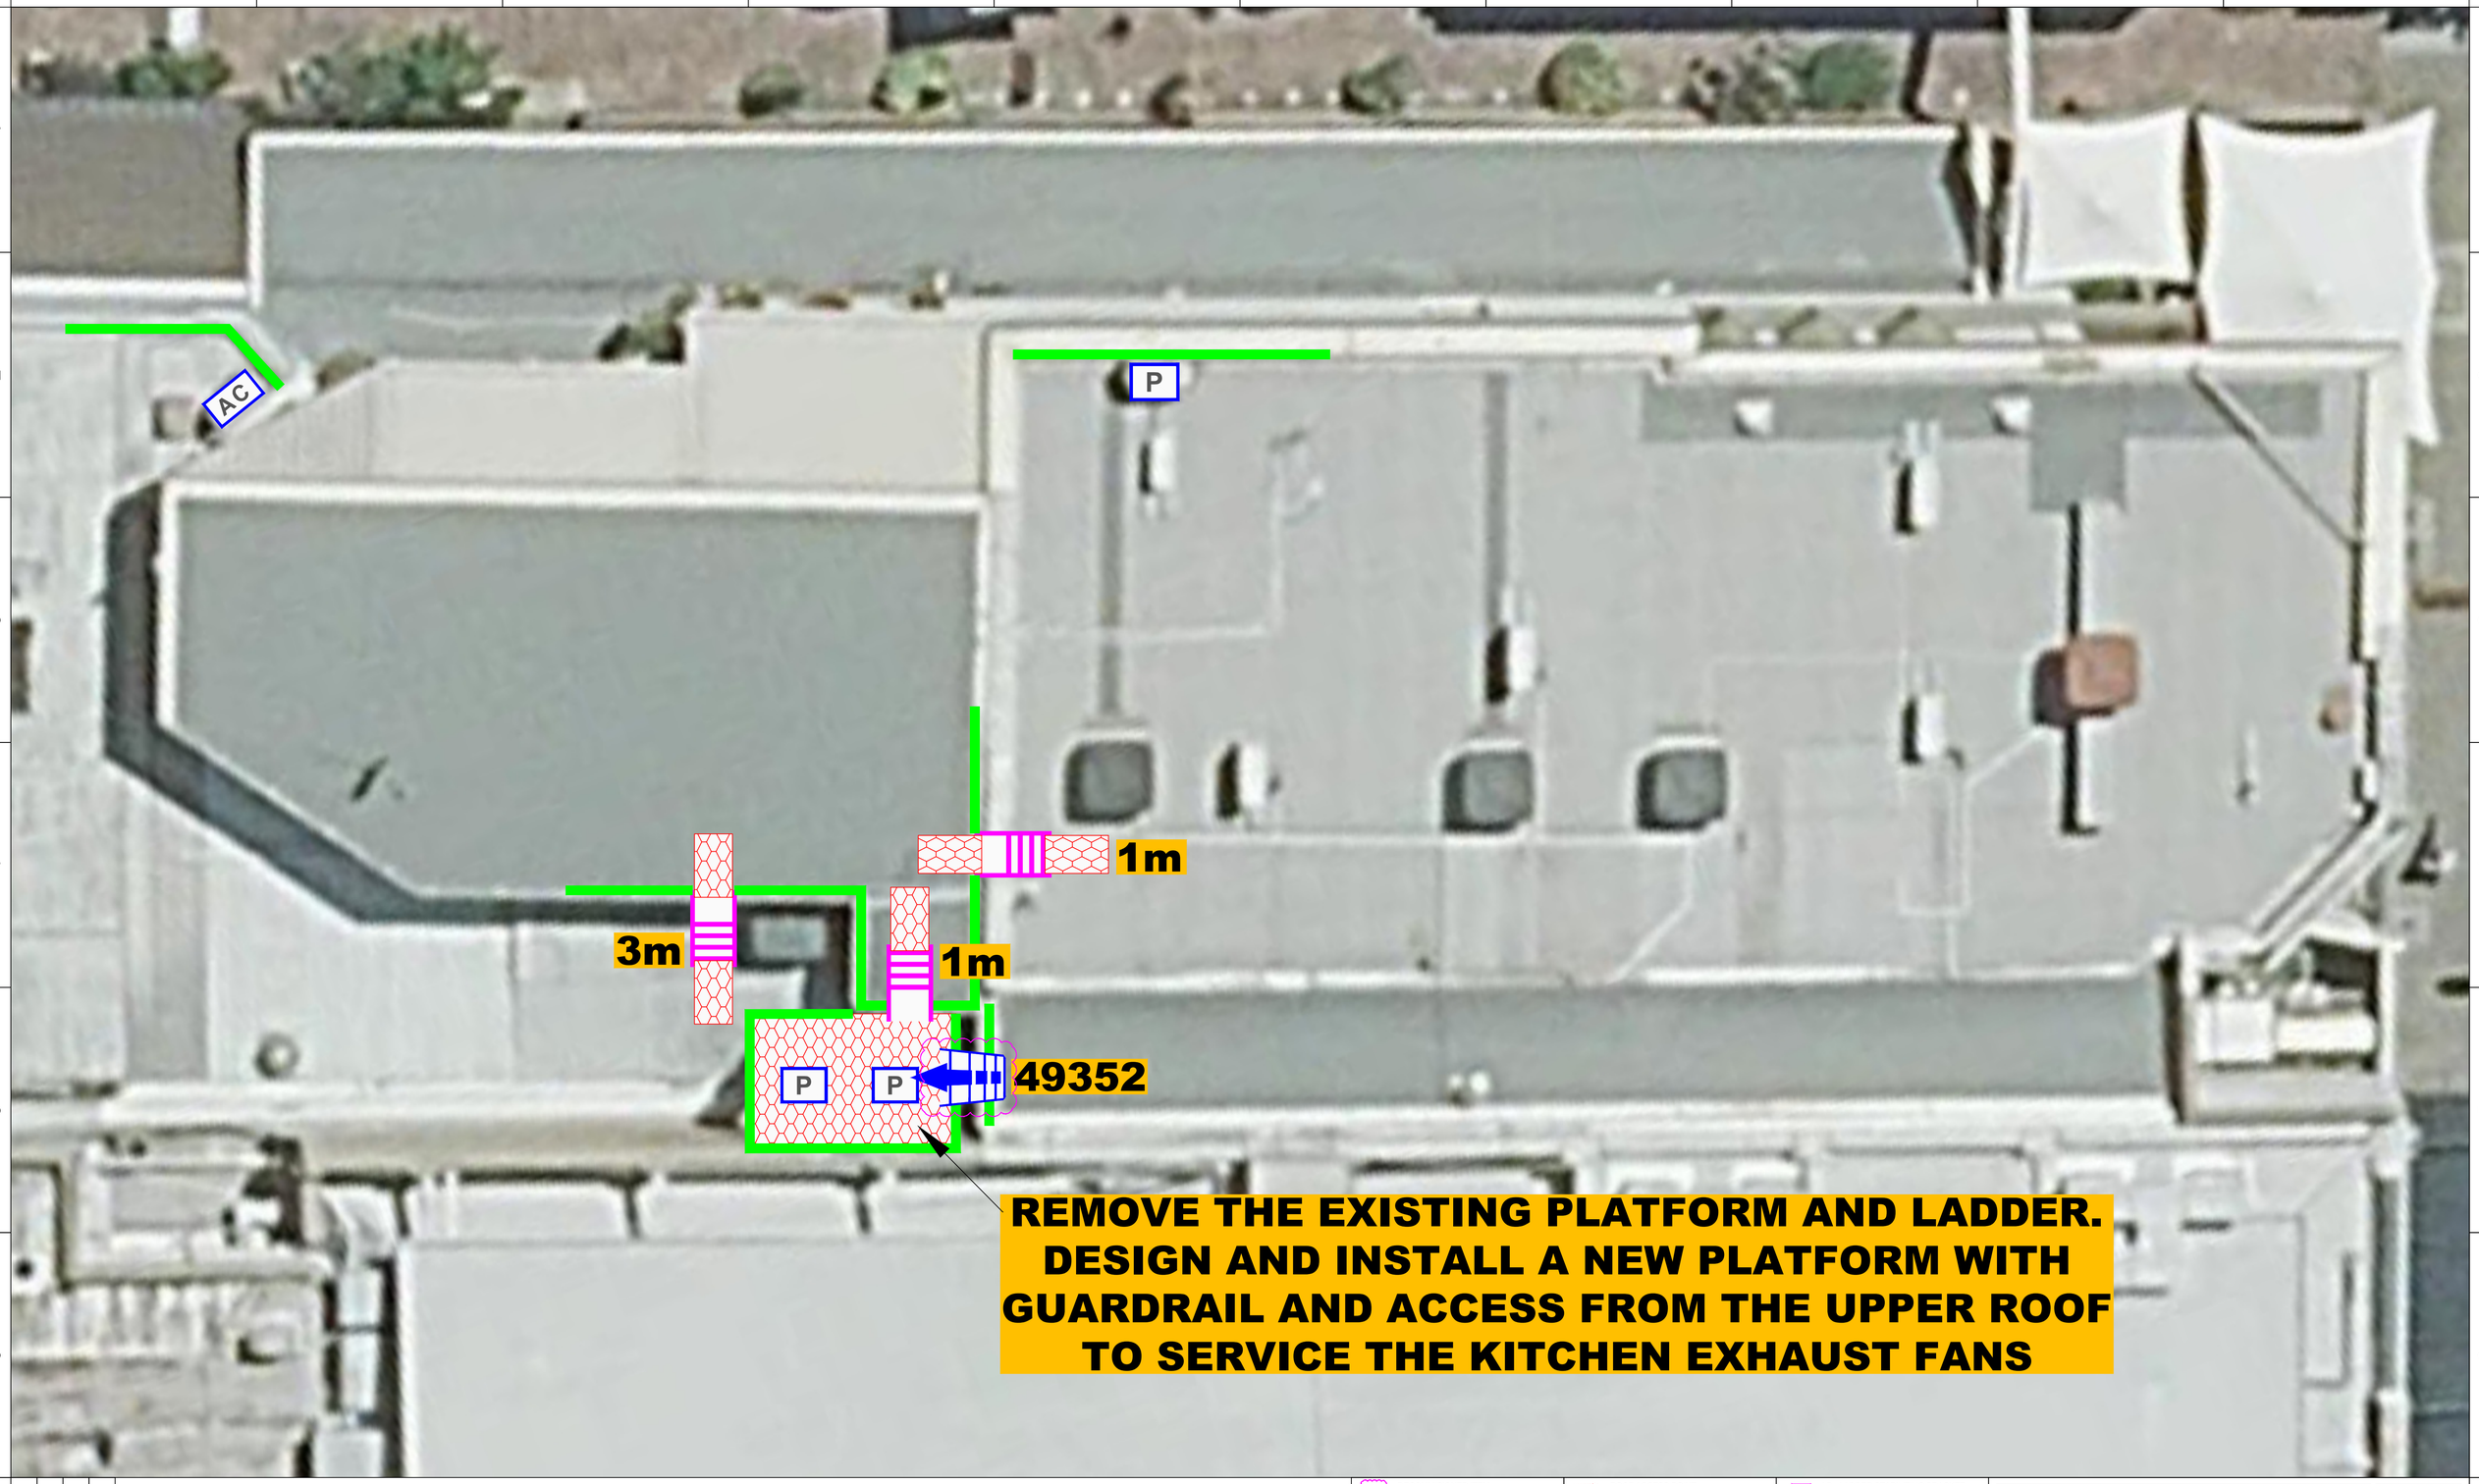


Rev	DESC.	Date
00	O3495 - Initial Release	18-03-2025

Existing line marking and signage is indicative only

N

DECOMMISIONED ITEM	ROOF ACCESS POINT	LB - LADDER STABILIZING BRACKET
DEMARCATION LINE	ACCESS HATCH WITH GUARDRAIL	CSL - STEP TYPE LADDER WITH CAGE
ANCHOR STROP	STAINLESS STEEL ANCHOR POINT	SL - STEP TYPE LADDER
ROOF ACCESS SIGNAGE	DAVIT SOCKET	CRL - RUNG LADDER WITH CAGE
TRAFFICABLE LASERLITE COVER	ROOF NEEDLE	RL - RUNG TYPE LADDER
	STL - STAINLESS STEEL STATIC LINE	STEP BRIDGE OVER PARAPET
	RR - ALUMINIUM MONORAIL SYSTEM	WALKWAY FLAT
	ALUMINIUM GUARDRAIL	SP - WALKWAY PLATFORM
	SELF CLOSING GATE	ST - STAIRWAY
	ACCESS FROM THE GROUND	SS - SINGLE STEP
	HIGH RISK AREA - NO ACCESS	SKYLIGHT PROTECTION
	SAFETY SIGNAGE	BLUE COLOUR DENOTES EXISTING SYSTEMS

workplace access&safety®
Independent, Practical, Compliance Partner

Australian Venue Co.

Drawing No: O3495

Company: Australian Venue Co.

Stage: Risk Assessment

Date: 18-03-2025

Site: TGS - The Generous Squire
397 Murray St, Perth WA 6000

Drawn: AS | Check: GC

Work area: Main Building

Site No: —

Scale: NTS

Verify all dimensions and site measure before commencing work. Do not scale from this drawing. This drawing is copyright and remains the property of Workplace Access and Safety and shall not be reproduced or copied in any format by any means without the written permissions of Workplace Access and Safety.

Template V 07.5/2020