


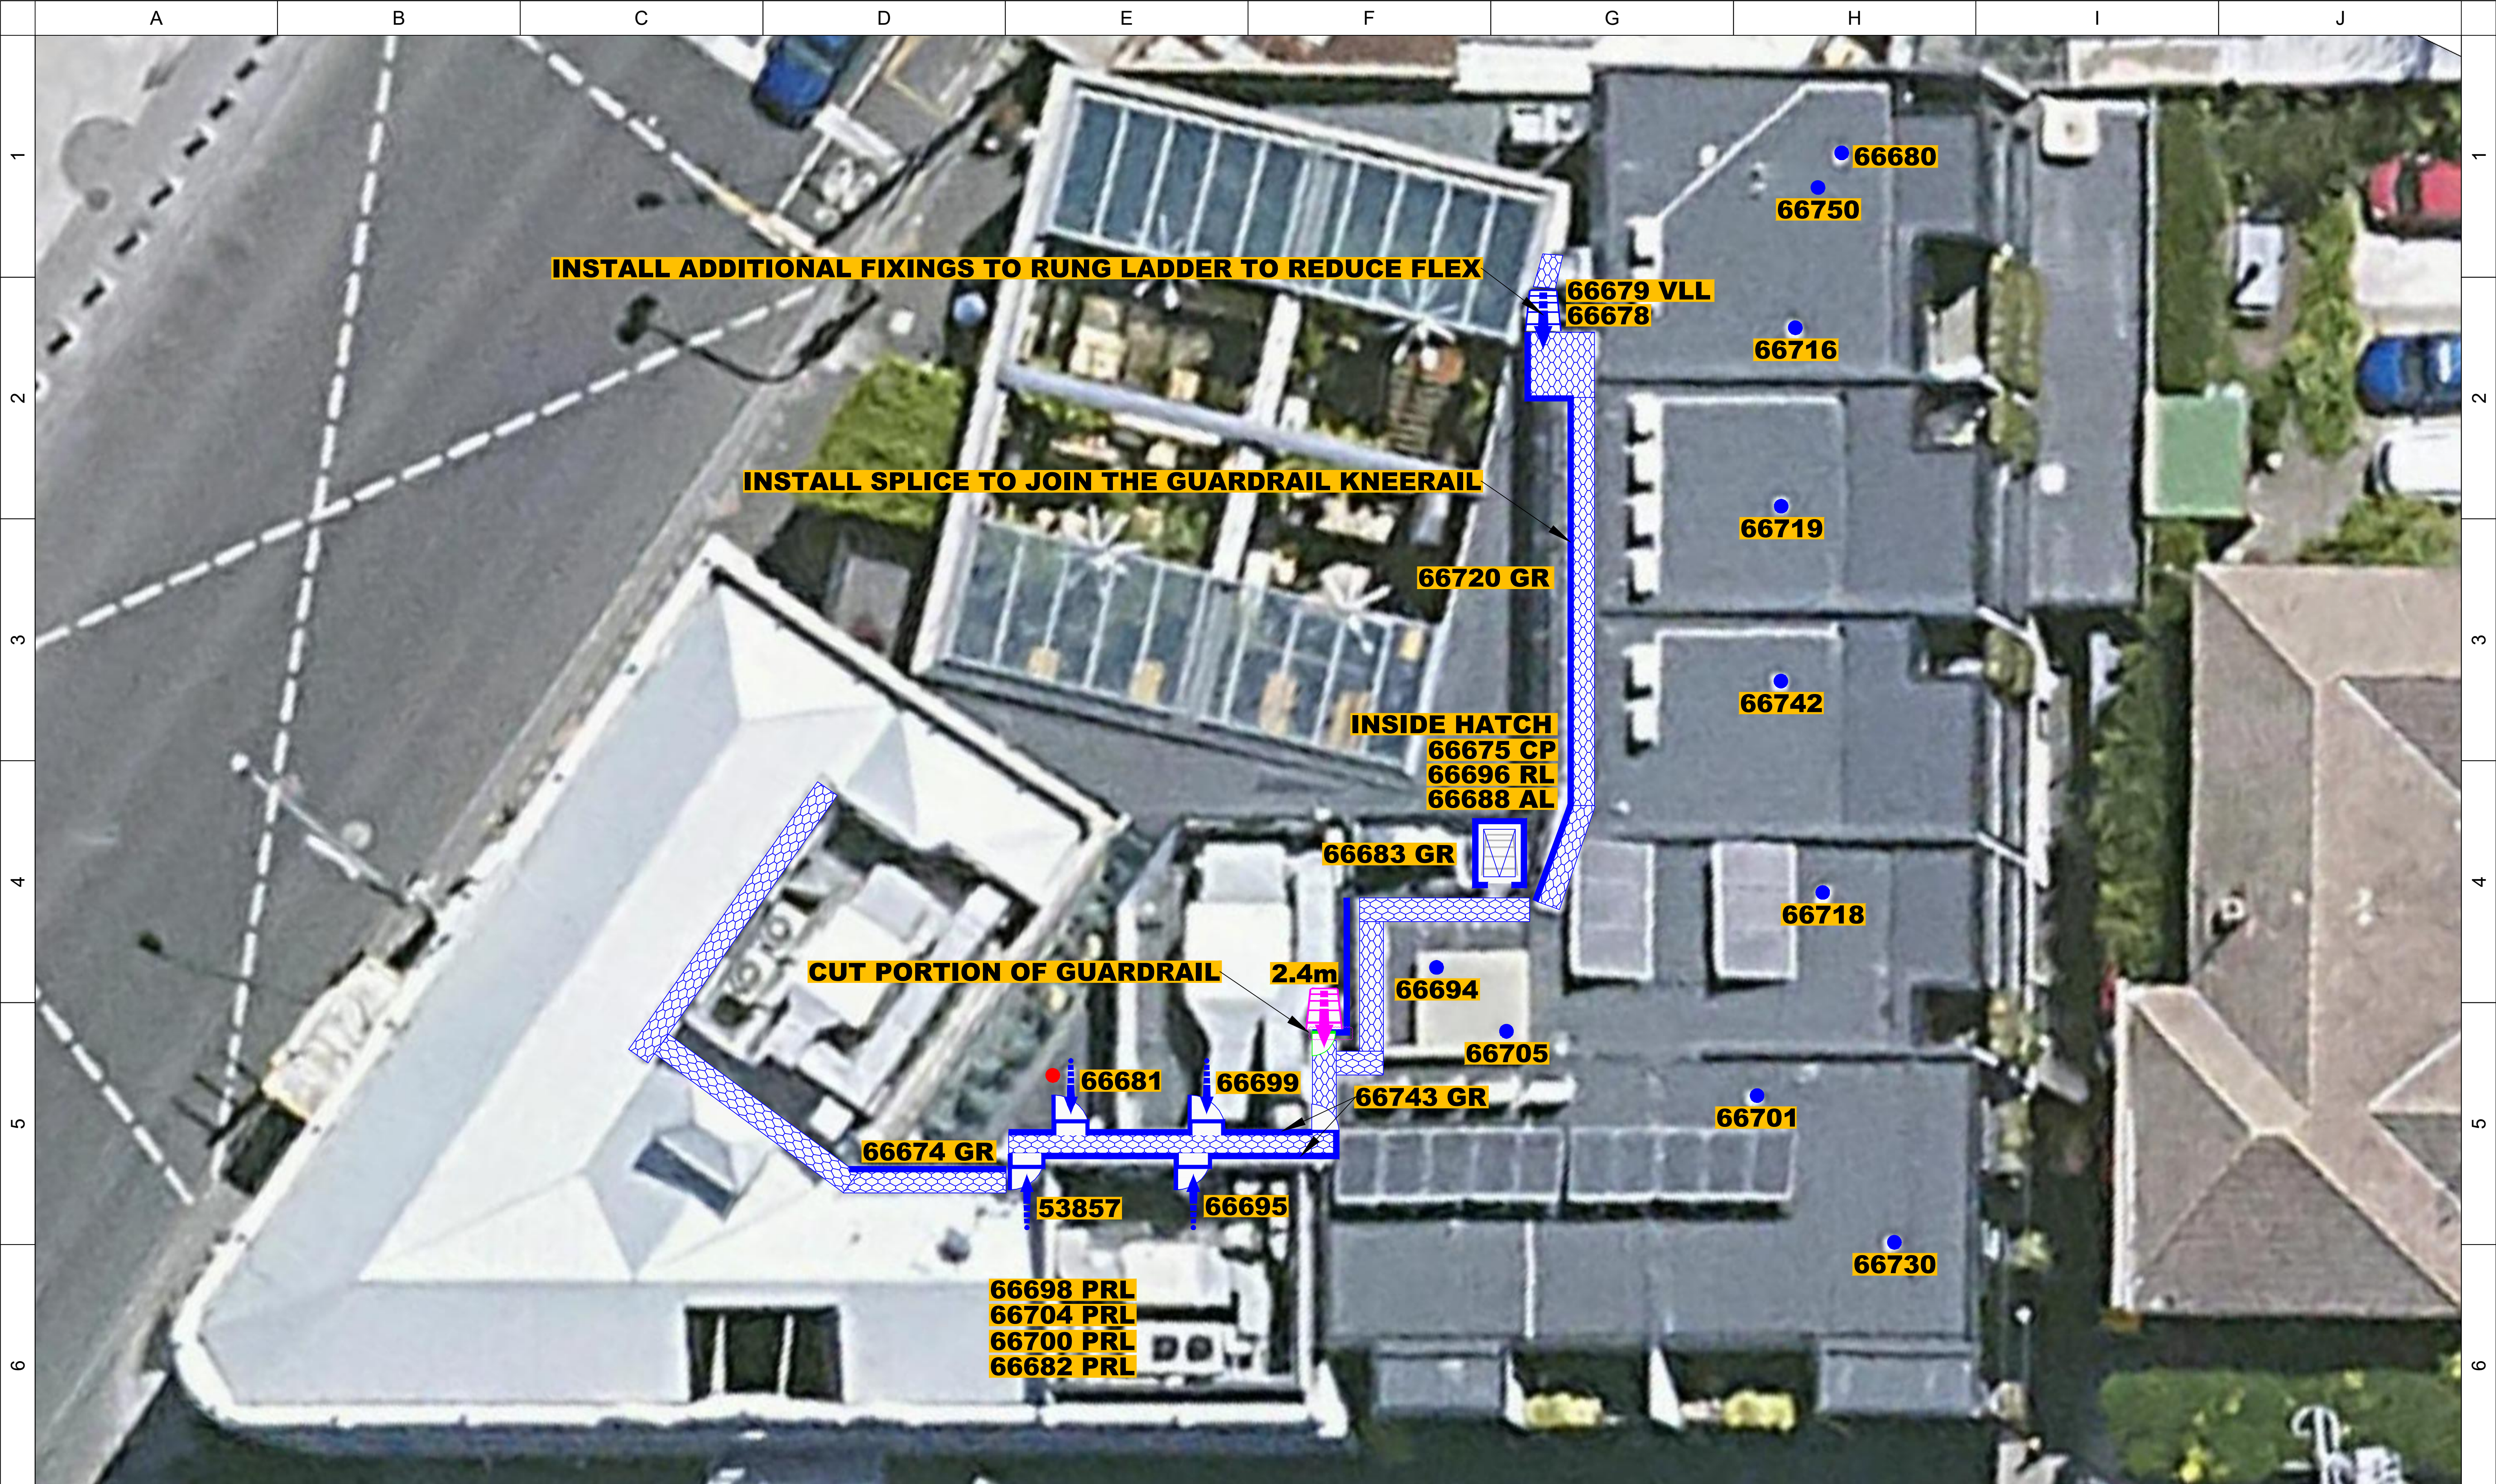

7	Date	28-02-2025	Existing line marking and signage is indicative only		<table border="1"><tr><td> DECOMMISSIONED ITEM</td><td> ROOF ACCESS POINT</td><td> LB - LADDER STABILIZING BRACKET</td></tr><tr><td> DEMARCATION LINE</td><td> ACCESS HATCH WITH GUARDRAIL</td><td> CSL - STEP TYPE LADDER WITH CAGE</td></tr><tr><td> ANCHOR STROP</td><td> STAINLESS STEEL ANCHOR POINT</td><td> SL - STEP TYPE LADDER</td></tr><tr><td> ROOF ACCESS SIGNAGE</td><td> DAVIT SOCKET</td><td> CRL - RUNG LADDER WITH CAGE</td></tr><tr><td>DESC.</td><td>03495 - Initial Release</td><td></td><td> TRAFFICABLE LASERLITE COVER</td><td> ROOF NEEDLE</td><td> RL - RUNG TYPE LADDER</td></tr><tr><td>Rev</td><td>00</td><td></td><td></td><td> STL - STAINLESS STEEL STATIC LINE</td><td> STEP BRIDGE OVER PARAPET</td></tr><tr><td></td><td></td><td></td><td></td><td> RR - ALUMINIUM MONORAIL SYSTEM</td><td> WALKWAY FLAT</td></tr><tr><td></td><td></td><td></td><td></td><td> ALUMINIUM GUARDRAIL</td><td> SP - WALKWAY PLATFORM</td></tr><tr><td></td><td></td><td></td><td></td><td> SELF CLOSING GATE</td><td> ST - STAIRWAY</td></tr><tr><td></td><td></td><td></td><td></td><td> ACCESS FROM THE GROUND</td><td> SS - SINGLE STEP</td></tr><tr><td></td><td></td><td></td><td></td><td> HIGH RISK AREA - NO ACCESS</td><td> SKYLIGHT PROTECTION</td></tr><tr><td></td><td></td><td></td><td></td><td> SAFETY SIGNAGE</td><td> BLUE COLOUR DENOTES EXISTING SYSTEMS</td></tr></table>			DECOMMISSIONED ITEM	ROOF ACCESS POINT	LB - LADDER STABILIZING BRACKET	DEMARCATION LINE	ACCESS HATCH WITH GUARDRAIL	CSL - STEP TYPE LADDER WITH CAGE	ANCHOR STROP	STAINLESS STEEL ANCHOR POINT	SL - STEP TYPE LADDER	ROOF ACCESS SIGNAGE	DAVIT SOCKET	CRL - RUNG LADDER WITH CAGE	DESC.	03495 - Initial Release		TRAFFICABLE LASERLITE COVER	ROOF NEEDLE	RL - RUNG TYPE LADDER	Rev	00			STL - STAINLESS STEEL STATIC LINE	STEP BRIDGE OVER PARAPET					RR - ALUMINIUM MONORAIL SYSTEM	WALKWAY FLAT					ALUMINIUM GUARDRAIL	SP - WALKWAY PLATFORM					SELF CLOSING GATE	ST - STAIRWAY					ACCESS FROM THE GROUND	SS - SINGLE STEP					HIGH RISK AREA - NO ACCESS	SKYLIGHT PROTECTION					SAFETY SIGNAGE	BLUE COLOUR DENOTES EXISTING SYSTEMS	<table border="1"><tr><td colspan="2"></td><td colspan="2"></td><td colspan="2">Drawing No: O3495</td></tr><tr><td colspan="6">Stage: Risk Assessment</td></tr><tr><td colspan="6">Date: 28/02/2025</td></tr><tr><td colspan="6">Drawn: AS</td></tr><tr><td colspan="6">Check: GC</td></tr><tr><td colspan="6">Scale: NTS</td></tr></table>						Drawing No: O3495		Stage: Risk Assessment						Date: 28/02/2025						Drawn: AS						Check: GC						Scale: NTS					
	DECOMMISSIONED ITEM	ROOF ACCESS POINT			LB - LADDER STABILIZING BRACKET	
	DEMARCATION LINE	ACCESS HATCH WITH GUARDRAIL			CSL - STEP TYPE LADDER WITH CAGE	
	ANCHOR STROP	STAINLESS STEEL ANCHOR POINT			SL - STEP TYPE LADDER	
ROOF ACCESS SIGNAGE	DAVIT SOCKET	CRL - RUNG LADDER WITH CAGE	
DESC.	03495 - Initial Release		TRAFFICABLE LASERLITE COVER	ROOF NEEDLE	RL - RUNG TYPE LADDER	
Rev	00			STL - STAINLESS STEEL STATIC LINE	STEP BRIDGE OVER PARAPET	
				RR - ALUMINIUM MONORAIL SYSTEM	WALKWAY FLAT	
				ALUMINIUM GUARDRAIL	SP - WALKWAY PLATFORM	
				SELF CLOSING GATE	ST - STAIRWAY	
				ACCESS FROM THE GROUND	SS - SINGLE STEP	
				HIGH RISK AREA - NO ACCESS	SKYLIGHT PROTECTION	
				SAFETY SIGNAGE	BLUE COLOUR DENOTES EXISTING SYSTEMS	
				Drawing No: O3495	
Stage: Risk Assessment	
Date: 28/02/2025	
Drawn: AS	
Check: GC	
Scale: NTS	
<table border="1"><tr><td colspan="2">Company: Australian Venue Co.</td><td colspan="2">Site: VBL - Village Belle Hotel 202 Barkly St, St Kilda VIC 3182</td></tr><tr><td colspan="2">Work area: Main Building</td><td colspan="2">Site No: </td></tr></table>					Company: Australian Venue Co.		Site: VBL - Village Belle Hotel 202 Barkly St, St Kilda VIC 3182		Work area: Main Building		Site No: 		Verify all dimensions and site measure before commencing work. Do not scale from this drawing. This drawing is copyright and remains the property of Workplace Access and Safety and shall not be reproduced or copied in any format by any means without the written permissions of Workplace Access and Safety. Template V 07.5/2020	
Company: Australian Venue Co.		Site: VBL - Village Belle Hotel 202 Barkly St, St Kilda VIC 3182	
Work area: Main Building		Site No: 	