


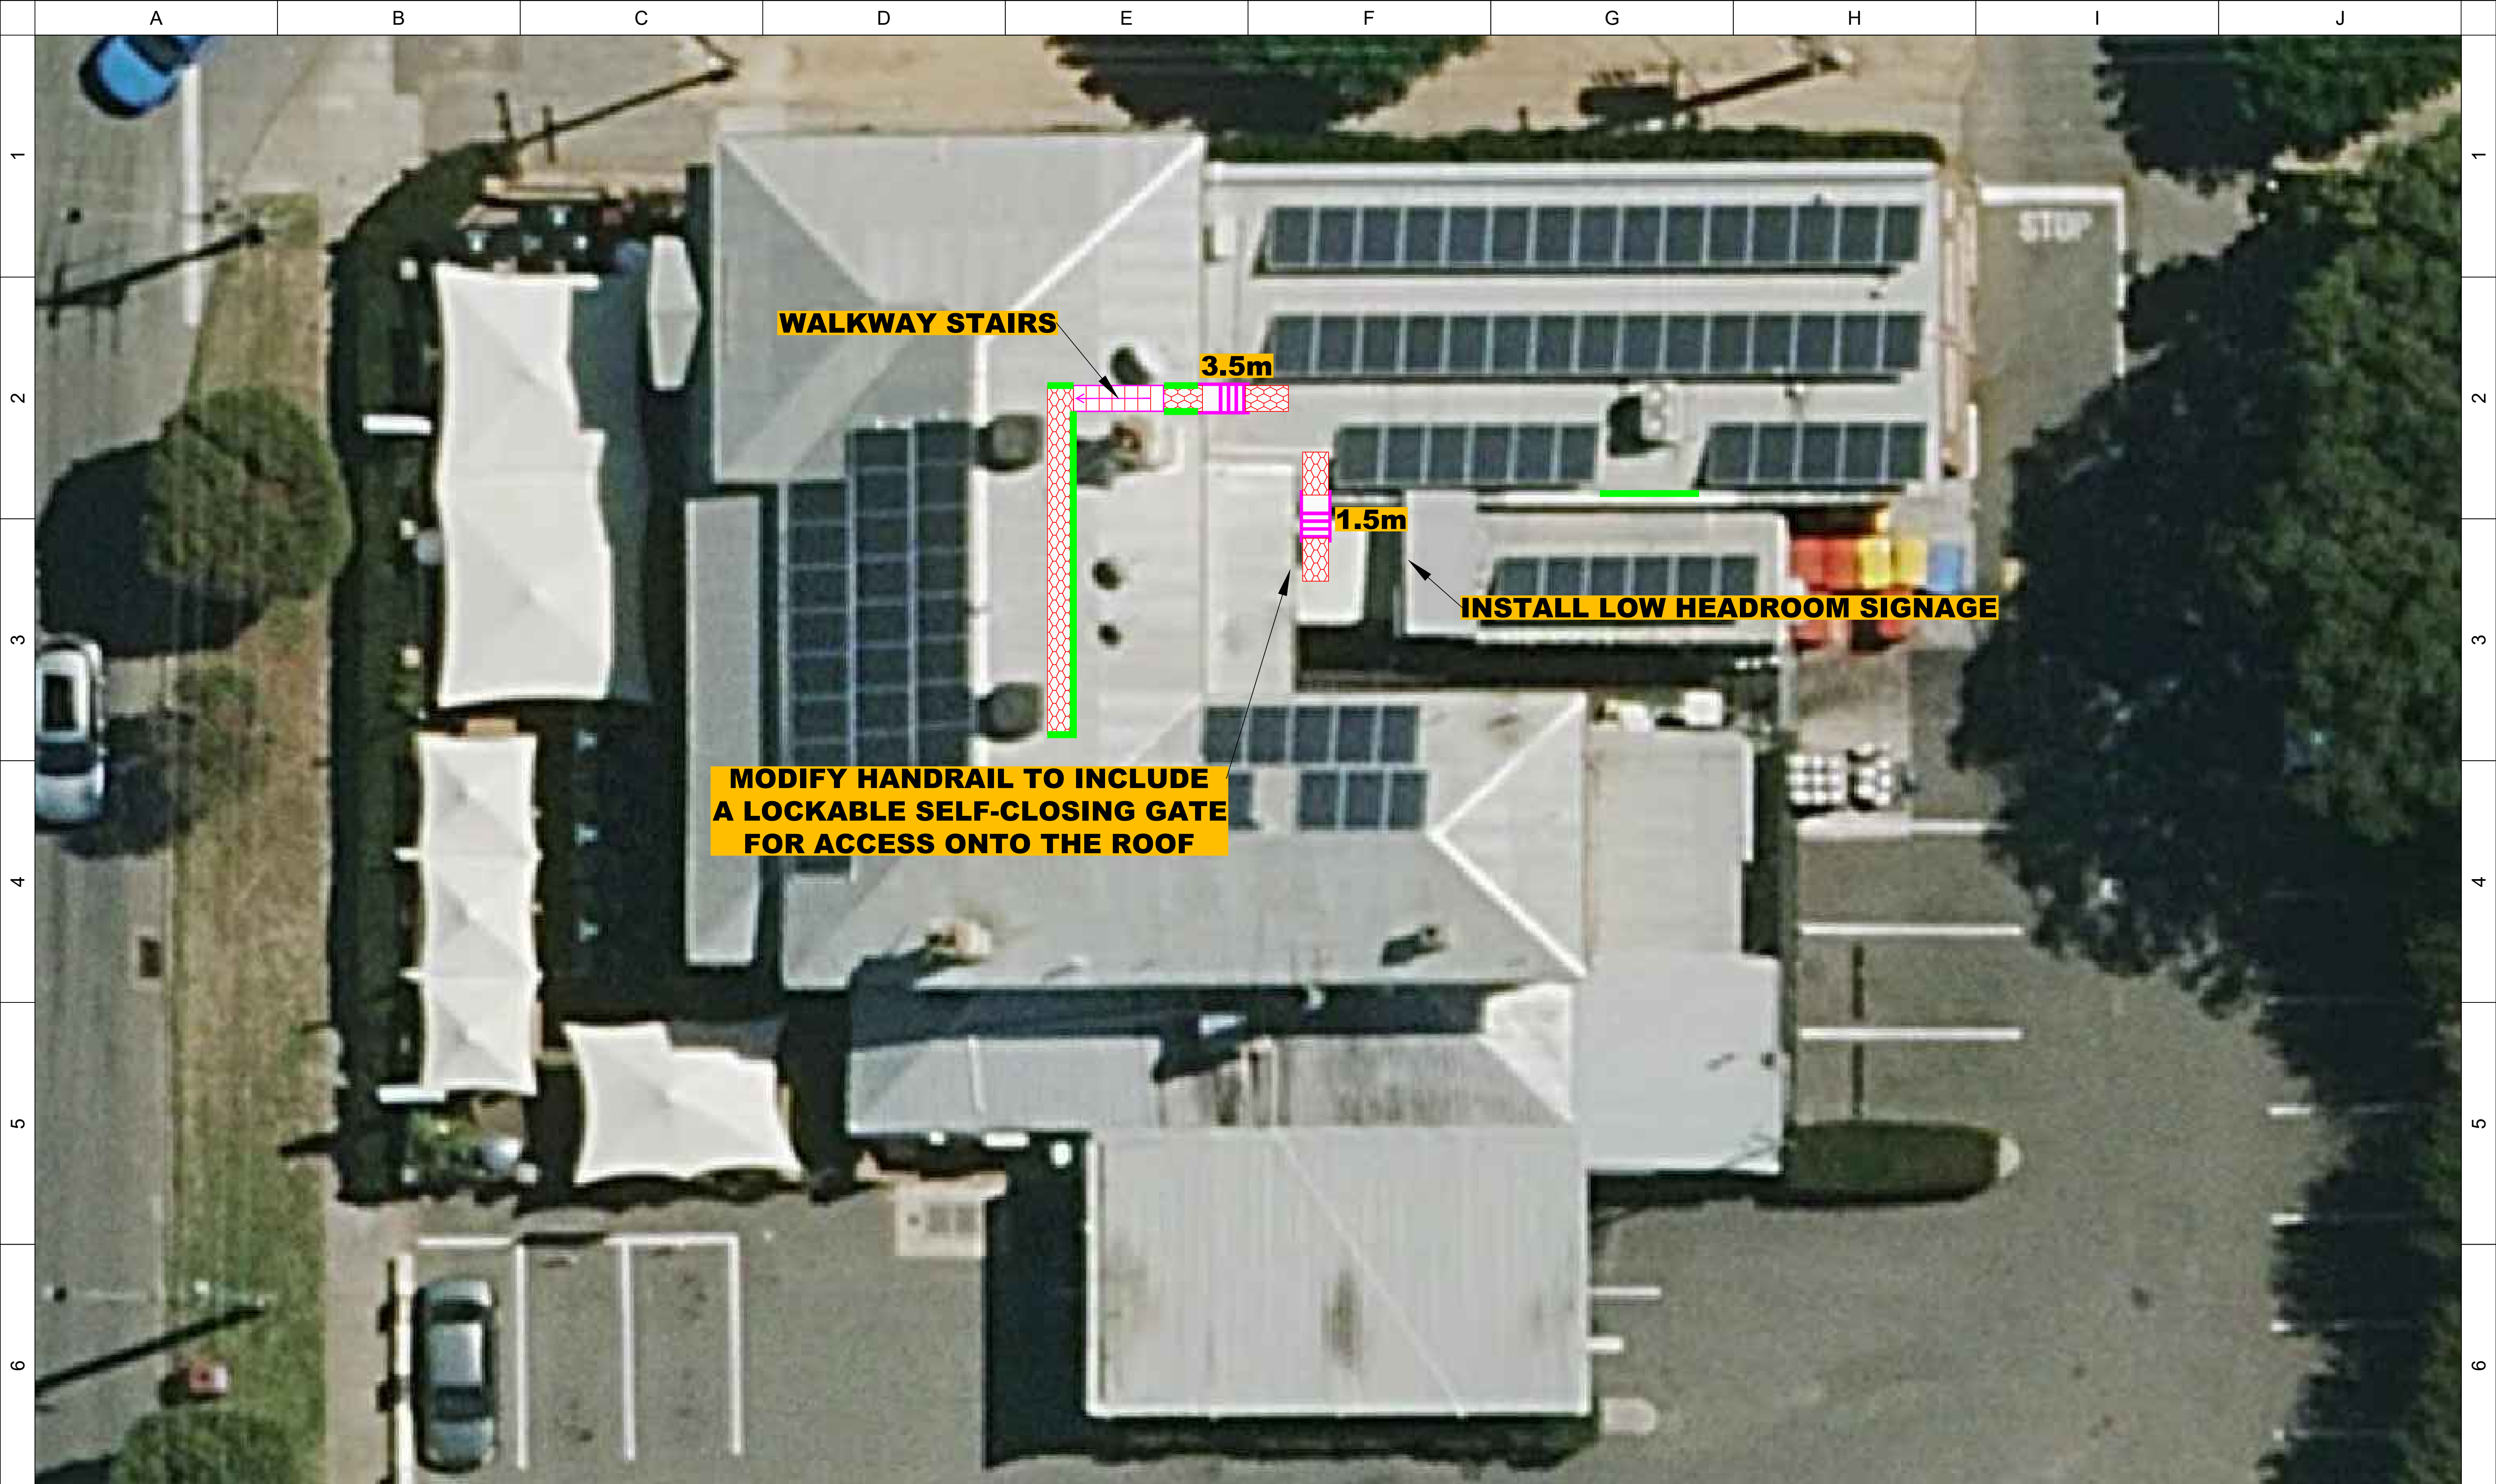

7

DESC.

Date

17-03-2025

Rev

00

O3495 - Initial Release

Existing line marking and signage is indicative only

N

	DECOMMISSIONED ITEM		ROOF ACCESS POINT		LB - LADDER STABILIZING BRACKET
	DEMARICATION LINE		ACCESS HATCH WITH GUARDRAIL		CSL - STEP TYPE LADDER WITH CAGE
	ANCHOR STROP		STAINLESS STEEL ANCHOR POINT		SL - STEP TYPE LADDER
	ROOF ACCESS SIGNAGE		DAVIT SOCKET		CRL - RUNG LADDER WITH CAGE
	TRAFFICABLE LASERLITE COVER		ROOF NEEDLE		RL - RUNG TYPE LADDER
			STL - STAINLESS STEEL STATIC LINE		STEP BRIDGE OVER PARAPET
			RR - ALUMINIUM MONORAIL SYSTEM		WALKWAY FLAT
			ALUMINIUM GUARDRAIL		SP - WALKWAY PLATFORM
			SELF CLOSING GATE		ST - STAIRWAY
			ACCESS FROM THE GROUND		SS - SINGLE STEP
			HIGH RISK AREA - NO ACCESS		SKYLIGHT PROTECTION
			SAFETY SIGNAGE		BLUE COLOUR DENOTES EXISTING SYSTEMS

Australian Venue Co.

Company:

Australian Venue Co.

Site:

WBR - Woodbridge Hotel
50 East St, Guildford WA 6055

Work area:

Main Building

Drawing No:

O3495

Stage:

Risk Assessment

Date:

17-03-2025

Drawn:

AS

Check:

GC

Scale:

NTS

Verify all dimensions and site measure before commencing work. Do not scale from this drawing. This drawing is copyright and remains the property of Workplace Access and Safety and shall not be reproduced or copied in any format by any means without the written permissions of Workplace Access and Safety.

Template V 07.5/2020

A

B

C

D

E

F

G

H

I

J