

QUOTATION

A.B.N.: 66 613 167 632

Quotation To:

Australian Venue Co.
Level 15, 242 Exhibition Street
Melbourne
VIC 3000

Site Address:

COU The Court
50 Beaufort St
Perth
WA 6000

Height Safety Consultant: Marco Tallarini

Quote No: 00023344

Quote Desc: Roof Rectification - The Court

Date: 2 March 2026

Main Building

Description	Qty
Install additional fixing to roof anchors	1
Main Building Total:	
	\$350.00

Upper Roof Plant Access

Description	Qty
Defender™ Portable Ladder Stabilising Bracket fixed to wall	1
Defender™ Rung ladder landing platform, levelled to substrate over 7 degree pitch.	1
Defender™ 13mm aluminium walkway levelled, with double guardrail system	6
Project Management, Site Mobilisation, Induction up to 1hr, Risk assessment and development of SWMS, Site Measure, Schematic layout approval, Final commission and inspection, Handover documentation	1
Vertical and horizontal lifting by hand, excludes Crane, Traffic management and permits if required	1
Freight to site including unloading of materials and manual handling	1
Upper Roof Plant Access Total:	
	\$10,506.55



Sub Total: \$10,856.55

GST: \$1,085.66

Total Inc GST: \$11,942.21

Quotation based on drawings supplied, to be confirmed upon site measure.


ACCEPTANCE OF QUOTATION:

1. Pending Payment in full, Workplace Defender shall retain title of all goods and materials either installed or delivered to you.
2. I have read the Conditions on the Contract and General Information attached to this Quotation and I agree thereto.
3. I accept the above Quotation and will pay the full amount shown and agreed to on completion of the work.

Print Name: _____

Date: _____

Signature: _____

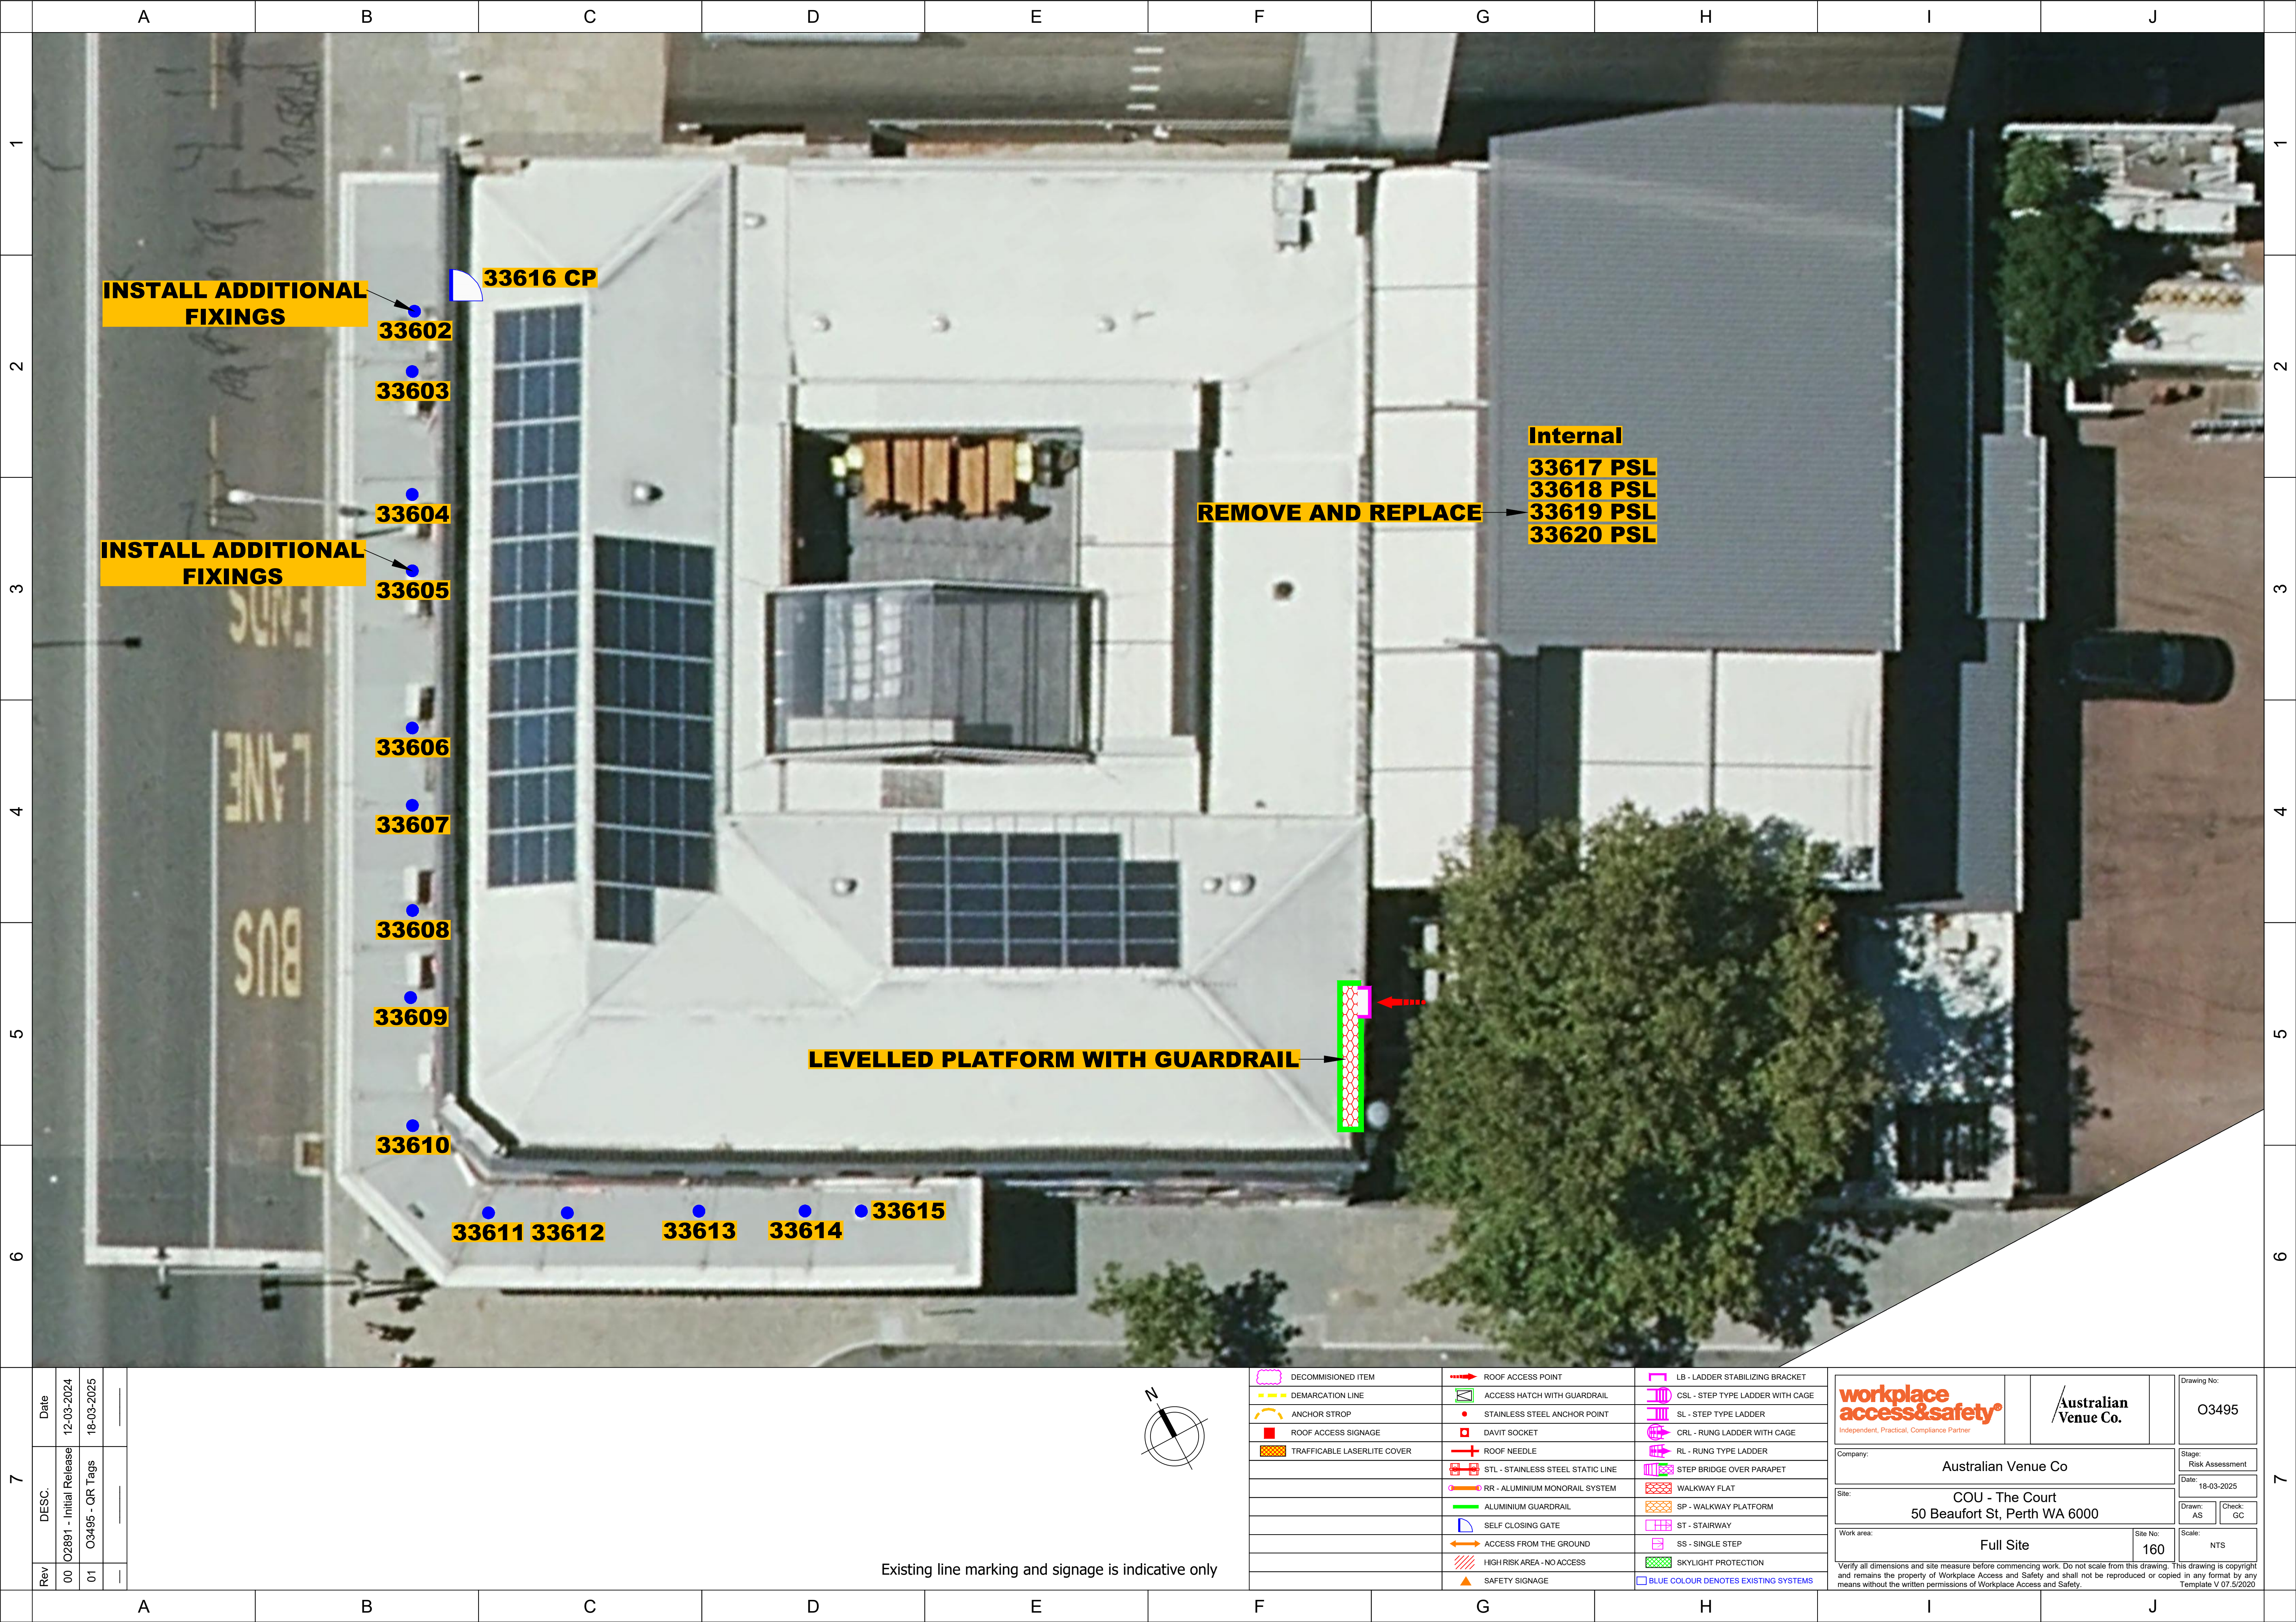

7			
Rev	DESC.	Date	
00	O2891 - Initial Release	12-03-2024	
01	O3495 - QR Tags	18-03-2025	
—	—	—	

Existing line marking and signage is indicative only



	DECOMMISSIONED ITEM		ROOF ACCESS POINT		LB - LADDER STABILIZING BRACKET
	DEMARICATION LINE		ACCESS HATCH WITH GUARDRAIL		CSL - STEP TYPE LADDER WITH CAGE
	ANCHOR STROP		STAINLESS STEEL ANCHOR POINT		SL - STEP TYPE LADDER
	ROOF ACCESS SIGNAGE		DAVIT SOCKET		CRL - RUNG LADDER WITH CAGE
	TRAFFICABLE LASERLITE COVER		ROOF NEEDLE		RL - RUNG TYPE LADDER
			STL - STAINLESS STEEL STATIC LINE		STEP BRIDGE OVER PARAPET
			RR - ALUMINIUM MONORAIL SYSTEM		WALKWAY FLAT
			ALUMINIUM GUARDRAIL		SP - WALKWAY PLATFORM
			SELF CLOSING GATE		ST - STAIRWAY
			ACCESS FROM THE GROUND		SS - SINGLE STEP
			HIGH RISK AREA - NO ACCESS		SKYLIGHT PROTECTION
			SAFETY SIGNAGE		BLUE COLOUR DENOTES EXISTING SYSTEMS

 <i>Independent, Practical, Compliance Partner</i>				Drawing No: O3495	
Company: Australian Venue Co				Stage: Risk Assessment	
Site: COU - The Court 50 Beaufort St, Perth WA 6000				Date: 18-03-2025	
Work area: Full Site				Drawn: AS	Check: GC
Site No: 160				Scale: NTS	
Verify all dimensions and site measure before commencing work. Do not scale from this drawing. This drawing is copyright and remains the property of Workplace Access and Safety and shall not be reproduced or copied in any format by any means without the written permissions of Workplace Access and Safety.					
Template V 07.5/2020					